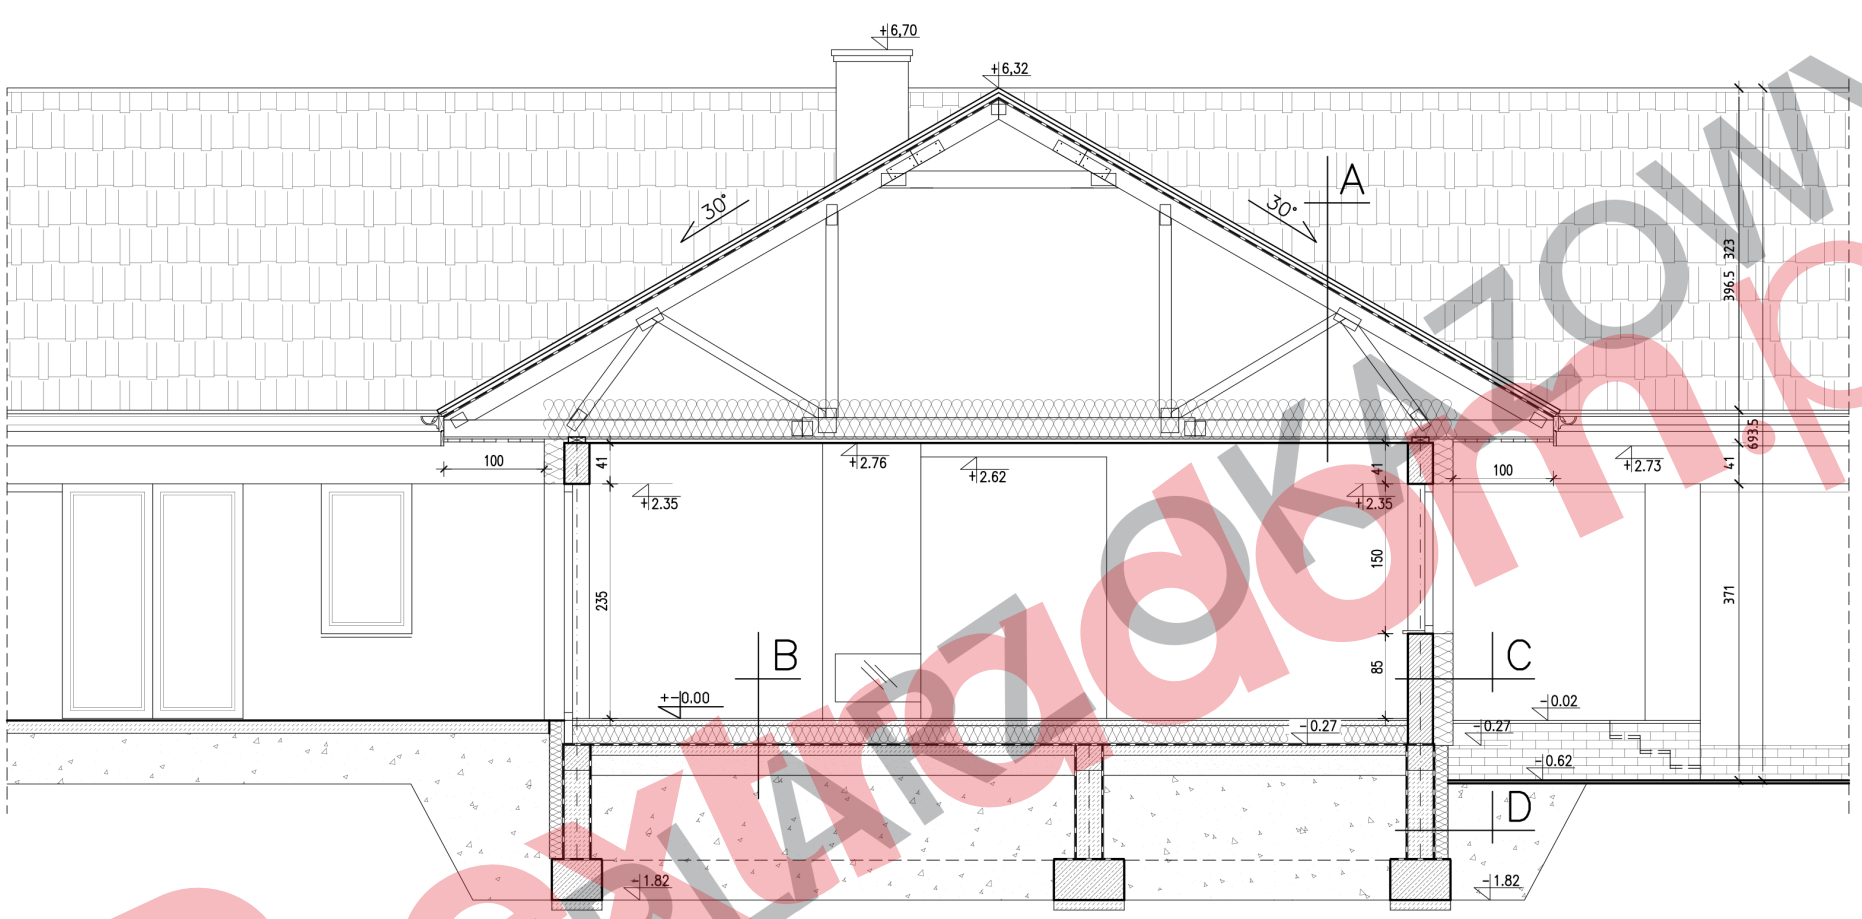



**A** DACH I STROP NAD PARTEREM
- BLACHODACHÓWKA
- ŁATY 4x5cm
- KONTRŁATY 2,5x5cm
- FOLIA ZBROJONA WSTĘPNEGO KRYCIA
- WIĄZAR DACHOWY PREFABRYKOWANY
- PUSTKA STROPOWA – WENTYLOWANA
- WEŁNA MIN. ISOVER Super Mata 40cm
- PAROIZOLACJA Z FOLII PE
- SUCHY TYNK NA RUSZCIE

**B** PODŁOGA PARTERU NA GRUNCIE
- DESKA PODŁOGOWA /TERAKOTA/ 2cm
- SZLICHTA BETONOWA 7cm ZBROJONA SIATKĄ PRZECIWSKURCZOWO
- STYROPIAN TERMO ORGANIKA TERMONIUM DACH–PODŁOGA gr.18cm
- IZOLACJA Z FOLII BUDOWLANEJ x2
- PODKŁAD BETONOWY 10cm
- UBITY PIASEK /ŻWIR/ 20cm

**C** ŚCIANA ZEWNĘTRZNA WYK. TYNKIEM
- TYNK CEM.–WAP.1.5cm
- PUSTAK CERAMICZNY 25cm
- STYROPIAN TERMONIUM PLUS FASADA gr.20cm
- TYNK CIENKOWARSTWOWY NA SIATCE SZKLANEJ

**C'** ŚCIANA ZEWNĘTRZNA WYK. PŁYTKAMI ELEWACYJNYMI
- TYNK CEM.–WAP.1.5cm
- PUSTAK CERAMICZNY 25cm
- STYROPIAN TERMO ORGANIKA TERMONIUM PLUS FASADA gr. 20cm
- PŁYTKI ELEWACYJNE

**D** ŚCIANA FUNDAMENTOWA
- IZOLACJA SYSTEM EMULBIT EKO NA SIATCE
- BLOCZEK BETONOWY 25cm
- IZOLACJA SYSTEM EMULBIT EKO NA SIATCE
- STYROPIAN TERMO ORGANIKA TERMONIUM FUNDAMENT gr.15cm
- PŁYTKI ELEWACYJNE POWYŻEJ GRUNTU

**C''** ŚCIANA ZEWNĘTRZNA WYK. SZALÓWKĄ
- TYNK CEM.–WAP.1.5cm
- PUSTAK CERAMICZNY 25cm
- RUSZT WSPORCZY Z ŁAT I KONTRŁAT DREWN. 10x6cm MOCOWANY KRZYŻOWO /WEŁNA MIN. ISOVER Aku–Płyta 2x10cm UKŁADANA POMIĘDZY RUSZTEM
- WIATROIZOLACJA "WIATROSTOP"
- ŁATY DREWNIANE 2,5cm MOCOWANE PIONOWO /PUSTKA WENT. 2,5cm/
- SZALÓWKA DREWNIANA LUB WINYLOWA MOCOWANA POZIOMO 2cm

UWAGA:
- FUNDAMENTY I ELEMENTY KONSTRUKCYJNE WYKONAĆ ZGODNIE Z RYS. KONSTRUKCYJNYMI
- KOMINY I PRZEWODY WENTYLACYJNE OCIEPLIĆ W PRZESTRZENI DACHOWEJ WEŁNĄ MINERALNĄ

EGZEMPLARZ ARCHIWALNY
egzemplarz archiwalny



Niniejszy projekt jest wersją demonstracyjną projektu gotowego autorstwa pracowni projektowej Domy w Stylu. Jest on chroniony na mocy przepisów zawartych w ustawie o prawie autorskim i prawach pokrewnych z dnia 04.02.1994 (Dz. Ustaw nr 24 poz. 83 z dnia 23.02.1994 z późniejszymi zmianami). Wykorzystanie tego projektu do celów handlowych, dalszej odsprzedaży, reprodukowania, kopiowania w całości czy też częściowo bez wiedzy i zgody pracowni projektowej Domy w Stylu jest zabronione.