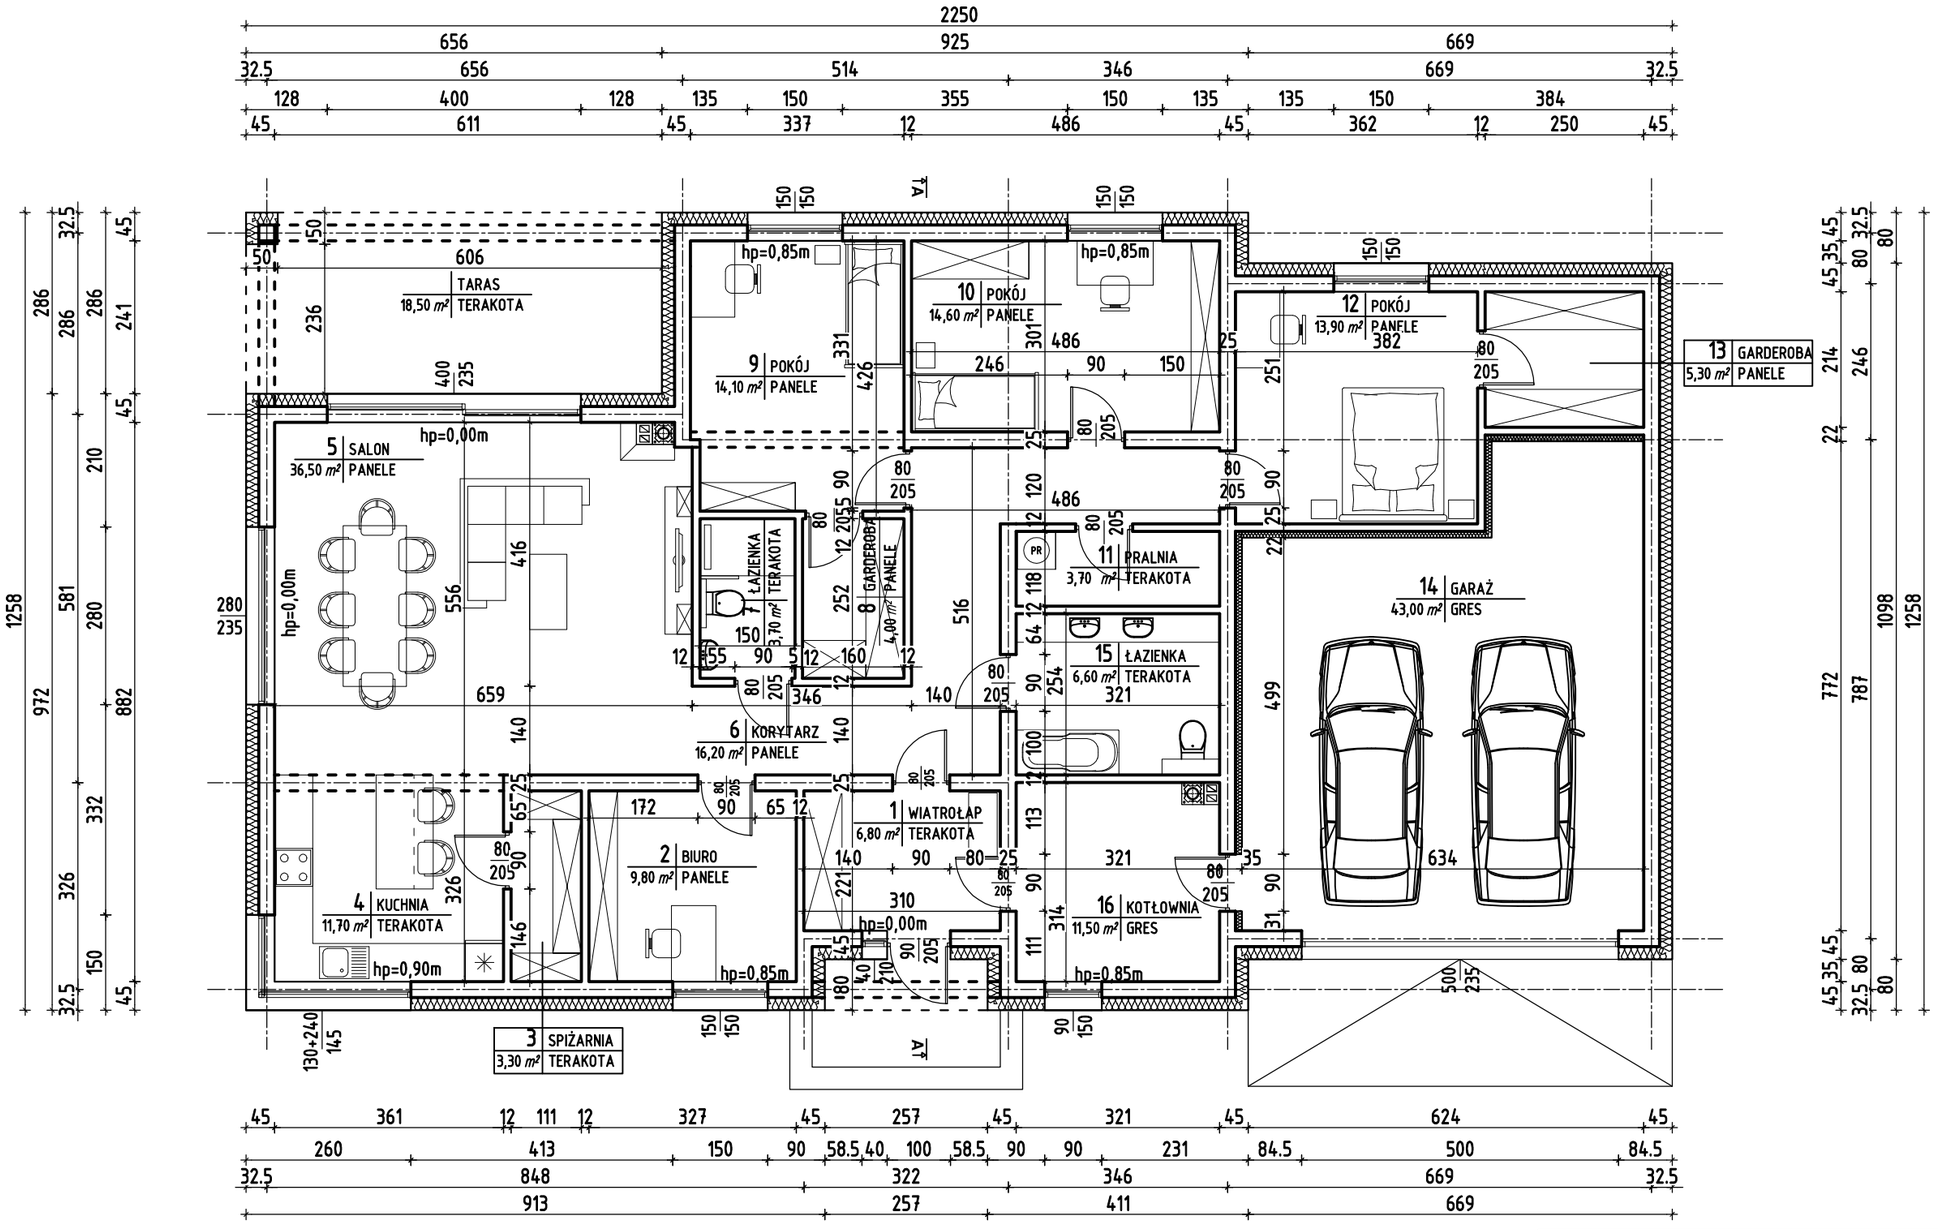



| | |
|---|---|
| 1 | WIATROŁAP 6,80 m² TERAKOTA |
| 2 | BIURO 9,80 m² PANELE |
| 3 | SPIŻARNIA 3,30 m² TERAKOTA |
| 4 | KUCHNIA 11,70 m² TERAKOTA |
| 5 | SALON 36,50 m² PANELE |
| 6 | KORYTARZ 16,20 m² PANELE |
| 7 | ŁAZIENKA 3,70 m² TERAKOTA |
| 8 | GARDEROBA 4,00 m² PANELE |
| 9 | POKÓJ 14,10 m² PANELE |
| 10 | POKÓJ 14,60 m² PANELE |
| 11 | PRALNIA 3,70 m² TERAKOTA |
| 12 | POKÓJ 13,90 m² PANELE |
| 13 | GARDEROBA 5,30 m² PANELE |
| 14 | GARAŻ 43,00 m² GRES |
| 15 | ŁAZIENKA 6,60 m² TERAKOTA |
| 16 | KOTŁOWNIA 11,50 m² GRES |

| | |
|---|---|
| POWIERZCHNIA ZABUDOWY: | 272,35 m² |
| POWIERZCHNIA UŻYTKOWA: | 204,70 m² |
| - MIESZKALNA | 150,20 m² |
| - GOSPODARCZA | 54,50 m² |
| KUBATURA BRUTTO: | 1 461,16 m³ |


JEDNOSTKA OPRACOWUJĄCA:
TE-DE SP.ZO.O.
ul. Nowy Świat 33/13; 00-029 Warszawa; tel. 605 255 383;
NIP 5252891372; mail: drozdzielpiotr@gmail.com


PT

INWESTOR:
DOMINIK I MARTA GRELA
UL. PIŁSUDSKIEGO 15A
23-400 BIŁGORAJ

NAZWA I ADRES OBIEKTU:
BUDOWA BUDYNKU MIESZKALNEGO JEDNORODZINNEGO WRAZ Z WEWNĘTRZNĄ INSTALACJĄ ELEKTRYCZNĄ, WODNĄ, KANALIZACJI SANITARNEJ, WENTYLACJI MECHANICZNEJ ORAZ ZEWNĘTRZNĄ INSTALACJĄ KABLOWĄ ELEKTROENERGETYCZNĄ NN ZALICZNIKOWĄ, INSTALACJĄ WODOCIĄGOWĄ I KANALIZACYJNĄ
dz. nr 95/9, AR_12; obręb ewidencyjny: 0001 BIŁGORAJ
jednostka ewidencyjna: 060201_1 BIŁGORAJ miasto


TYTUŁ RYSUNKU: RZUT PARTERU

SKALA: 1:100

| FUNKCJA | IMIĘ I NAZWISKO ORAZ ZAKRES I SPECJALNOŚĆ UPRAWNIEŃ | PODPIS |
|---|---|---|
| PROJEKTANT KONSTRUKCJA | mgr inż. Piotr Droździel<br>*upr. bud. do projektowania i kierowania robotami bez ograniczeń w specj. konstrukcyjno – budowlanej LUB/0364/PWBKb/15* | |

DATA: 12.2025


NR RYS.: 1

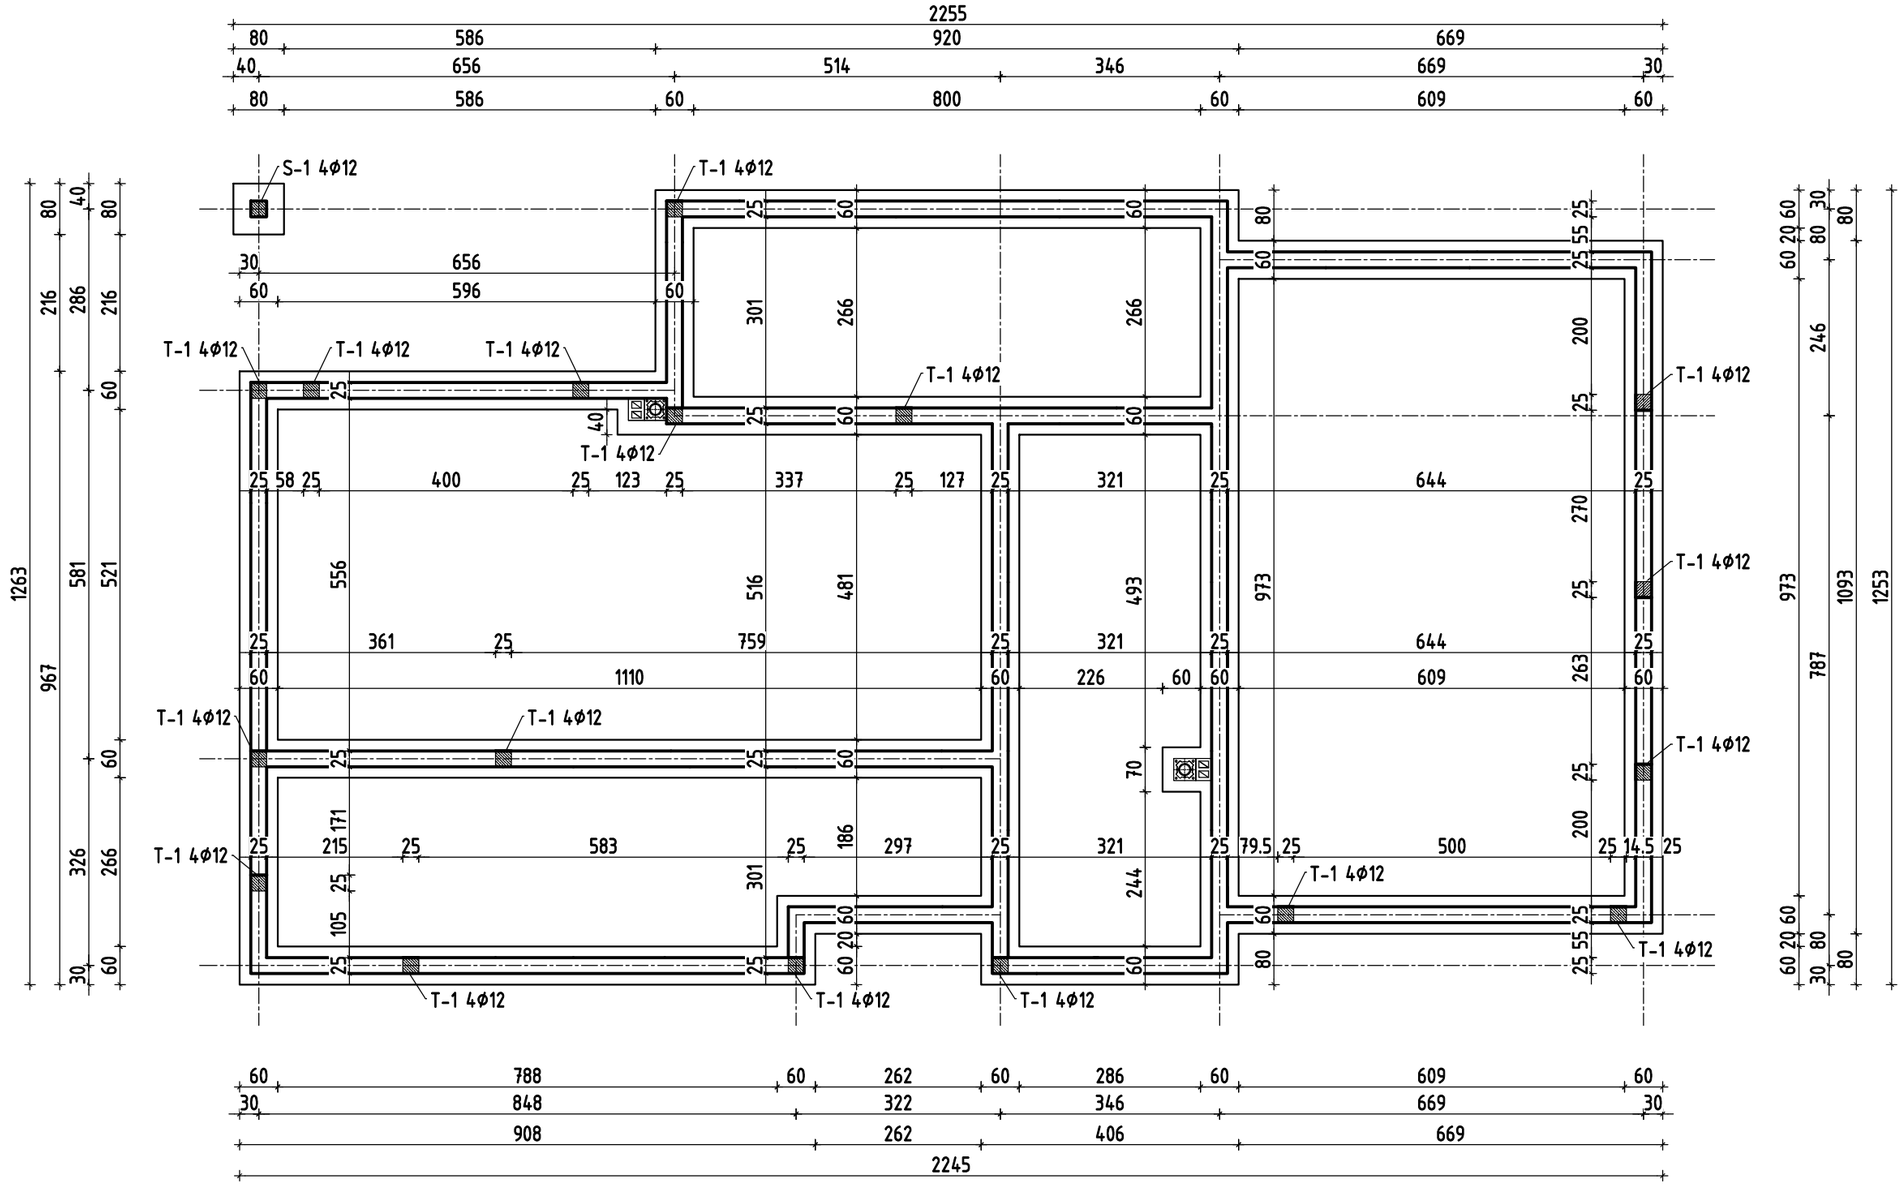



| | | | |
|---|---|---|---|
| JEDNOSTKA OPRACOWUJĄCA: TE-DE SP.Z O.O. ul. Nowy Świat 33/13; 00-029 Warszawa; tel. 605 255 383; NIP 5252891372; mail: drozdzielpiotr@gmail.com | | | PT |
| INWESTOR: DOMINIK I MARTA GRELA UL. PIŁSUDSKIEGO 15A 23-400 BIŁGORAJ | NAZWA I ADRES OBIEKTU: BUDOWA BUDYNKU MIESZKALNEGO JEDNORODZINNEGO WRAZ Z WEWNĘTRZNĄ INSTALACJĄ ELEKTRYCZNĄ, WODNĄ, KANALIZACJI SANITARNEJ, WENTYLACJI MECHANICZNEJ ORAZ ZEWNĘTRZNĄ INSTALACJĄ KABLOWĄ ELEKTROENERGETYCZNĄ NN ZALICZNIKOWĄ, INSTALACJĄ WODOCIĄGOWĄ I KANALIZACYJNĄ dz. nr 95/9, AR_12; obręb ewidencyjny: 0001 BIŁGORAJ jednostka ewidencyjna: 060201_1 BIŁGORAJ miasto | | |
| TYTUŁ RYSUNKU | RZUT ŁAW FUNDAMENTOWYCH | | SKALA 1:100 |
| FUNKCJA | IMIĘ I NAZWISKO ORAZ ZAKRES I SPECJALNOŚĆ UPRAWNIEŃ | PODPIS | |
| PROJEKTANT KONSTRUKCJA | mgr inż. Piotr Droździel *upr. bud. do projektowania i kierowania robotami bez ograniczeń w specj. konstrukcyjno – budowlanej LUB/0364/PWBKb/15* | | DATA 12.2025 |
| | | | NR RYS. 2 |


# PRZEKROJE FUNDAMENTÓW
# SKALA 1:20

Ława fundam. ŁF–1
Skala 1:20

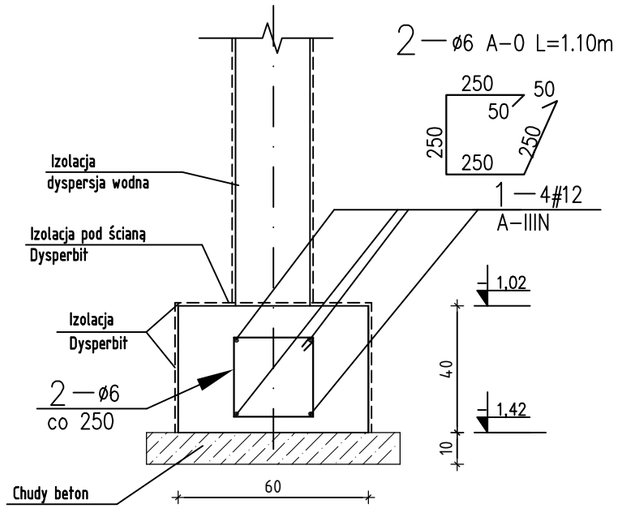


Stopa fundam. ST–1
Skala 1:20

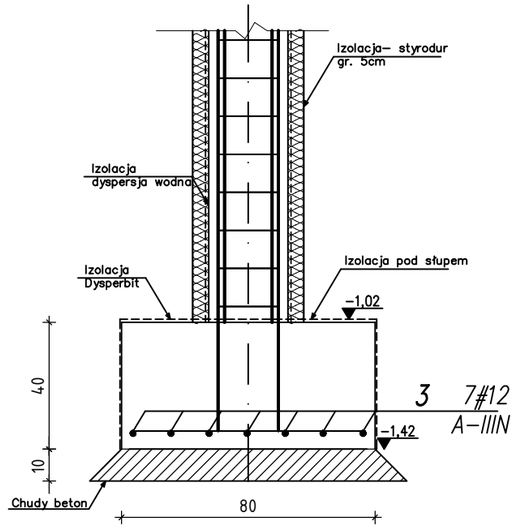

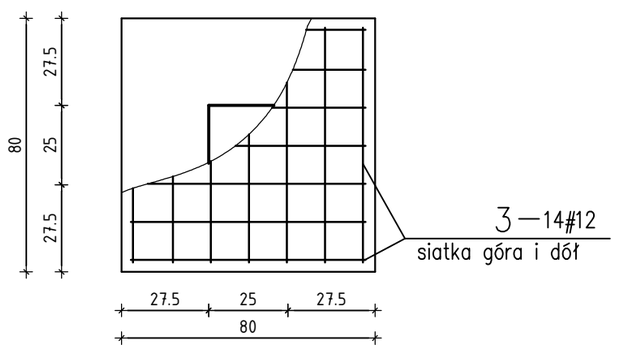
| | |
|---|---|
| Beton | C20/25 (B25) |
| Stal zbrojeniowa | A–IIIN (RB500W) |
| Stal strzemion | A–0 (St–0) |
| Otulina | 5cm |
| Izolacja | Dysperbit |
| Chudy beton | C8/10 (B10) |

UWAGI:
1. Izolacje przeciwwodne wykonać zgodnie z opisem technicznym.
2. Wszystkie fundamenty zwymiarowano przyjmując naprężenia dopuszczalne w gruncie 200kPa.
3. Zbrojenie podłużne ław należy łączyć ze sobą na zakład Długość zakładu prętów #12 – 500mm



JEDNOSTKA OPRACOWUJĄCA:
TE-DE SP.Z O.O.
ul. Nowy Świat 33/13; 00–029 Warszawa; tel. 605 255 383;
NIP 5252891372; mail: drozdzielpiotr@gmail.com


PT

INWESTOR:
DOMINIK I MARTA GRELA
UL. PIŁSUDSKIEGO 15A
23–400 BIŁGORAJ

NAZWA I ADRES OBIEKTU:
BUDOWA BUDYNKU MIESZKALNEGO JEDNORODZINNEGO WRAZ Z WEWNĘTRZNĄ INSTALACJĄ ELEKTRYCZNĄ, WODNĄ, KANALIZACJI SANITARNEJ, WENTYLACJI MECHANICZNEJ ORAZ ZEWNĘTRZNĄ INSTALACJĄ KABLOWĄ ELEKTROENERGETYCZNĄ NN ZALICZNIKOWĄ, INSTALACJĄ WODOCIĄGOWĄ I KANALIZACYJNĄ
dz. nr 95/9, AR_12; obręb ewidencyjny: 0001 BIŁGORAJ
jednostka ewidencyjna: 060201_1 BIŁGORAJ miasto

| TYTUŁ RYSUNKU | ZBROJENIE FUNDAMENTÓW | SKALA 1:20 |
|---|---|---|
| FUNKCJA | IMIĘ I NAZWISKO ORAZ ZAKRES I SPECJALNOŚĆ UPRAWNIEŃ | PODPIS |
| PROJEKTANT KONSTRUKCJA | mgr inż. Piotr Drożdziel<br>*upr. bud. do projektowania i kierowania robotami bez ograniczeń w specj. konstrukcyjno – budowlanej LUB/0364/PWBKb/15* | DATA 12.2025 |
| | | NR RYS. 3 |

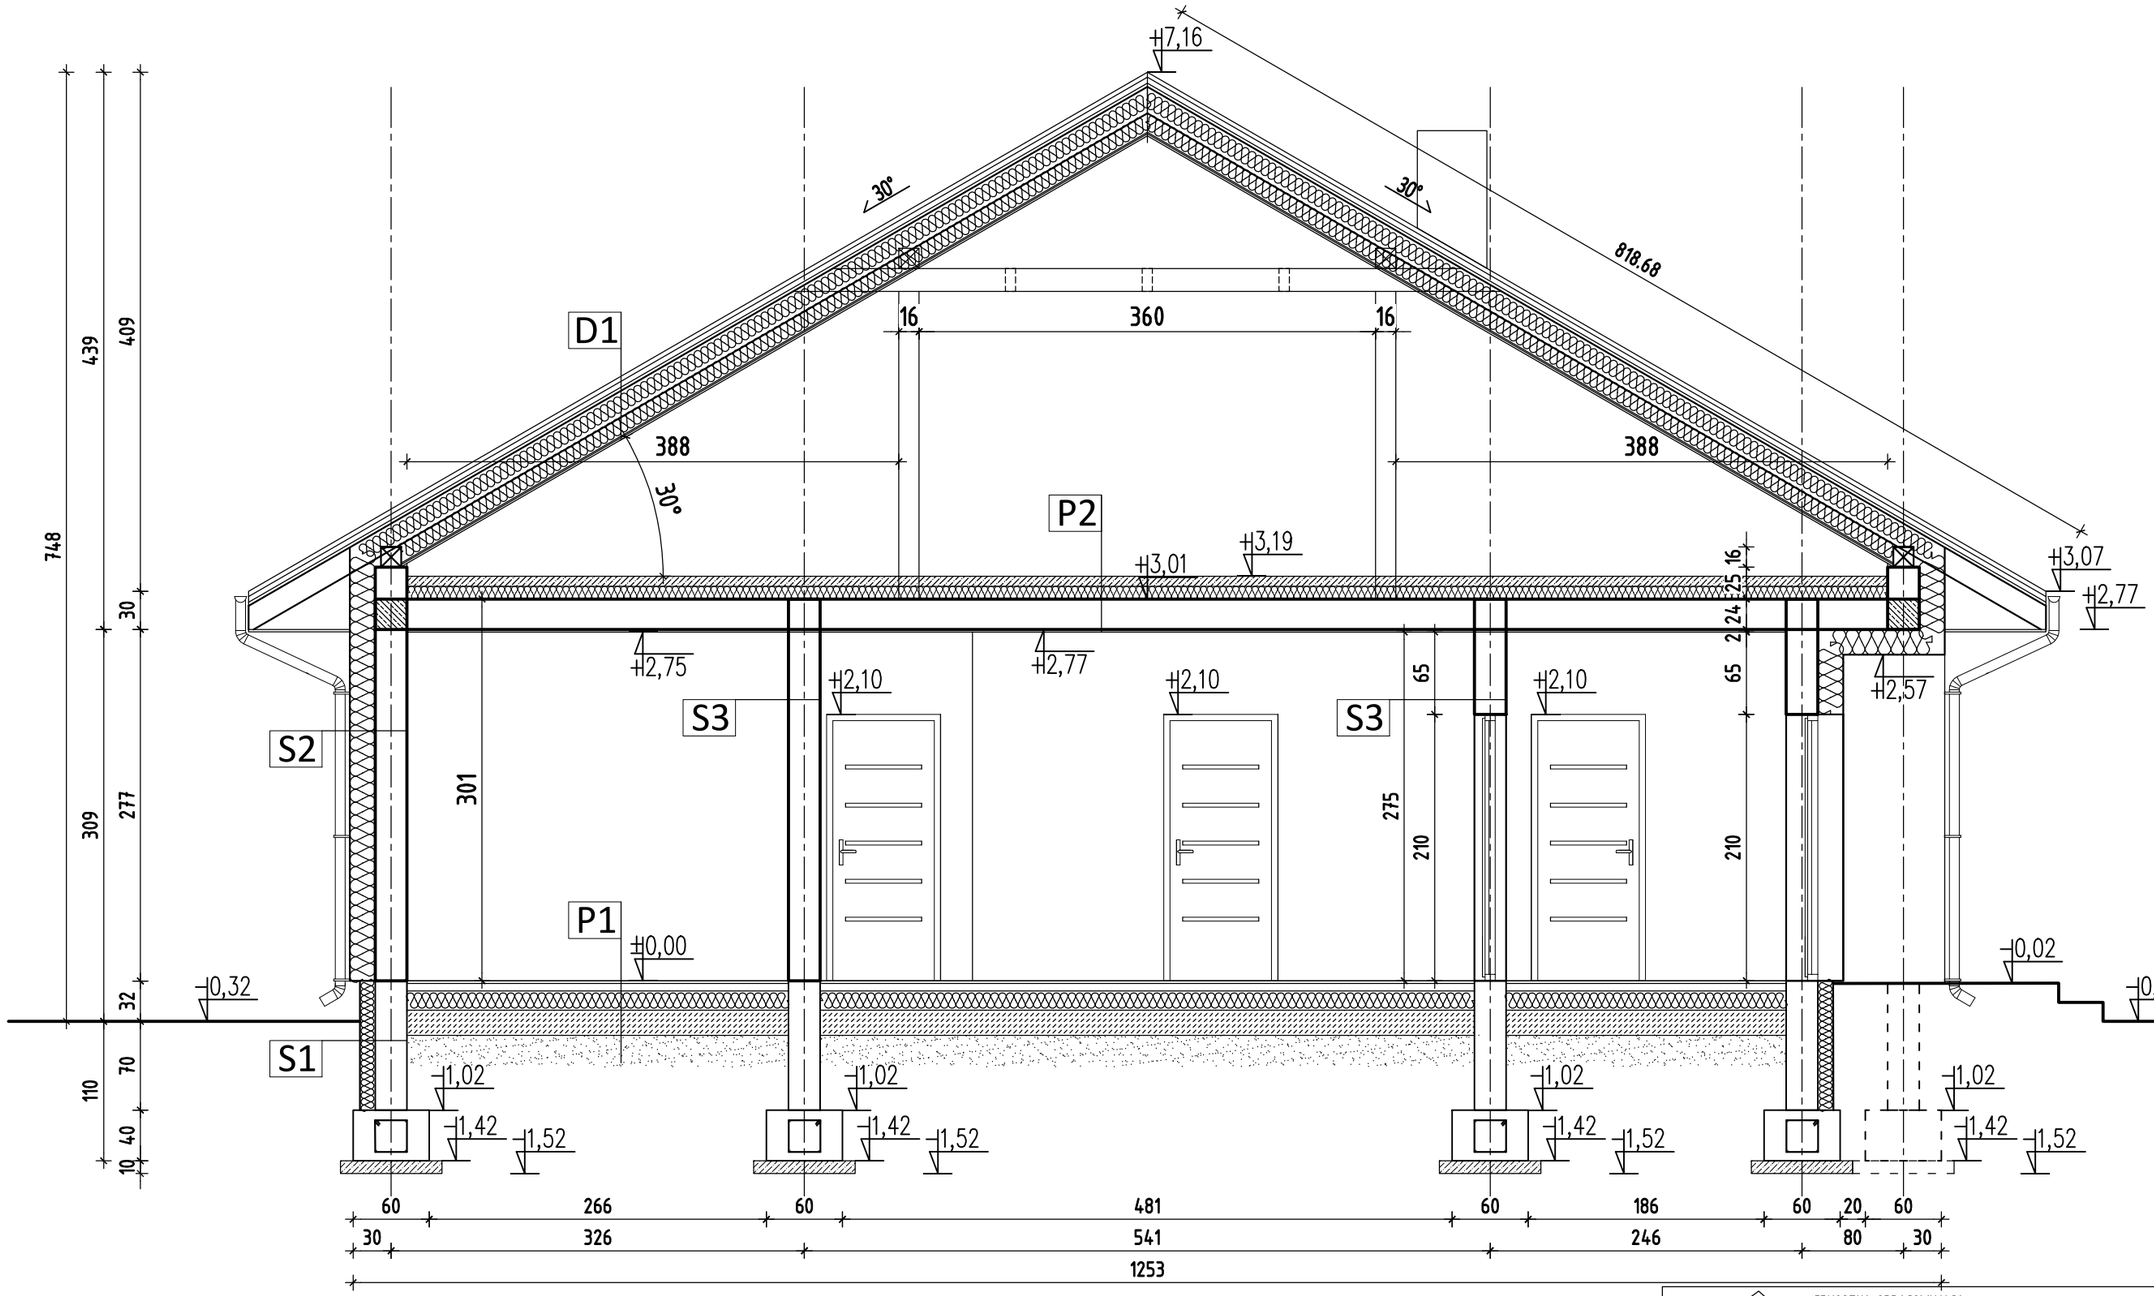


| S1 | ŚCIANA FUNDAMENTOWA | |
|---|---|---|
| | STYROPIAN FUNDAMENTOWY EPS 100-036 | 12 cm |
| | IZOLACJA PRZECIWILGOCIOWA, NP. IZOBUD WL, IZOHAN | |
| | BLOCZKI BETONOWE gr. 25cm, beton C25/30 | 25cm |
| | IZOLACJA PRZECIWILGOCIOWA, NP. IZOBUD WL, IZOHAN | |

| S2 | ŚCIANA ZEWNĘTRZNA | |
|---|---|---|
| | TYNK CEMENTOWO-WAPIENNY KAT. III (wewnątrz) | 1,5cm |
| | PUSTAK GAZOBETONOWY na zaprawie cem-wap | 25cm |
| | STYROPIAN EPS 40-032 | 20cm |
| | KLEJ ZBROJONY SIATKĄ Z WŁÓKNA SZKLANEGO | 0,5cm |
| | TYNK STRUKTURALNY SILIKATOWO-SILIKONOWY | 0,5cm |

| S3 | ŚCIANA WEWNĘTRZNA NOŚNA | |
|---|---|---|
| | TYNK CEMENTOWO-WAPIENNY KAT. III | 1,5cm |
| | PUSTAK GAZOBETONOWY na zaprawie cem-wap | 25cm |
| | TYNK CEMENTOWO-WAPIENNY KAT. III | 1,5cm |

| P1 | POSADZKA NA GRUNCIE | |
|---|---|---|
| | WYLEWKA CEMENTOWA | 5cm |
| | FOLIA PE 0,2mm | 2x |
| | STYROPIAN EPS 100-038 gr. 10cm | 15cm |
| | 2x FOLIA PE 0,2mm | 2x |
| | WYLEWKA BETONOWA | 2x |
| | PODSYPKA Z KRUSZYWA 0/2 f3 wg PN-EN 13242+A1:2010 wyrównana, | |
| | o zagęszczeniu Ev2>90 MPa, Ev2/Ev1<2,5 | 25cm |
| | GRUNT RODZIMY | |

| P2 | POSADZKA NA STROPIE | |
|---|---|---|
| | TYNK CEMENTOWO-WAPIENNY KAT. III | 1,5cm |
| | STROP TERIVA | 24cm |
| | STYROPIAN EPS 100-038 GR. 20cm | 10cm |
| | 2x FOLIA PE 0,2mm | 2x |
| | WYLEWAKA SAMOPOZIOMUJĄCA | 6cm |

| D1 | DACH | |
|---|---|---|
| | BLACHODACHÓWKA | 3,5cm |
| | Łaty 40x50mm | 4cm |
| | Kontrłaty 25x50mm | 2,5cm |
| | Membrana dachowa | - |
| | Krokiew 8x18cm / Wełna mineralna 30cm | 18cm / 12cm |


JEDNOSTKA OPRACOWUJĄCA:
TE-DE SP.ZO.O.
ul. Nowy Świat 33/13; 00-029 Warszawa; tel. 605 255 383;
NIP 5252891372; mail: drozdzielpiotr@gmail.com


PT

INWESTOR:
DOMINIK I MARTA GRELA
UL. PIŁSUDSKIEGO 15A
23-400 BIŁGORAJ

NAZWA I ADRES OBIEKTU:
BUDOWA BUDYNKU MIESZKALNEGO JEDNORODZINNEGO WRAZ Z WEWNĘTRZNĄ INSTALACJĄ ELEKTRYCZNĄ, WODNĄ, KANALIZACJI SANITARNEJ, WENTYLACJI MECHANICZNEJ ORAZ ZEWNĘTRZNĄ INSTALACJĄ KABLOWĄ ELEKTROENERGETYCZNĄ NN ZALICZNIKOWĄ, INSTALACJĄ WODOCIĄGOWĄ I KANALIZACYJNĄ
dz. nr 95/9, AR_12; obręb ewidencyjny: 0001 BIŁGORAJ
jednostka ewidencyjna: 060201_1 BIŁGORAJ miasto


TYTUŁ RYSUNKU: PRZEKRÓJ A-A

SKALA 1:50


| FUNKCJA | IMIĘ I NAZWISKO ORAZ ZAKRES I SPECJALNOŚĆ UPRAWNIEŃ | PODPIS |
|---|---|---|
| PROJEKTANT KONSTRUKCJA | mgr inż. Piotr Drożdziel<br>*upr. bud. do projektowania i kierowania robotami bez ograniczeń w specj. konstrukcyjno – budowlanej LUB/0364/PWBKb/15* | |

DATA 12.2025

NR RYS. 4

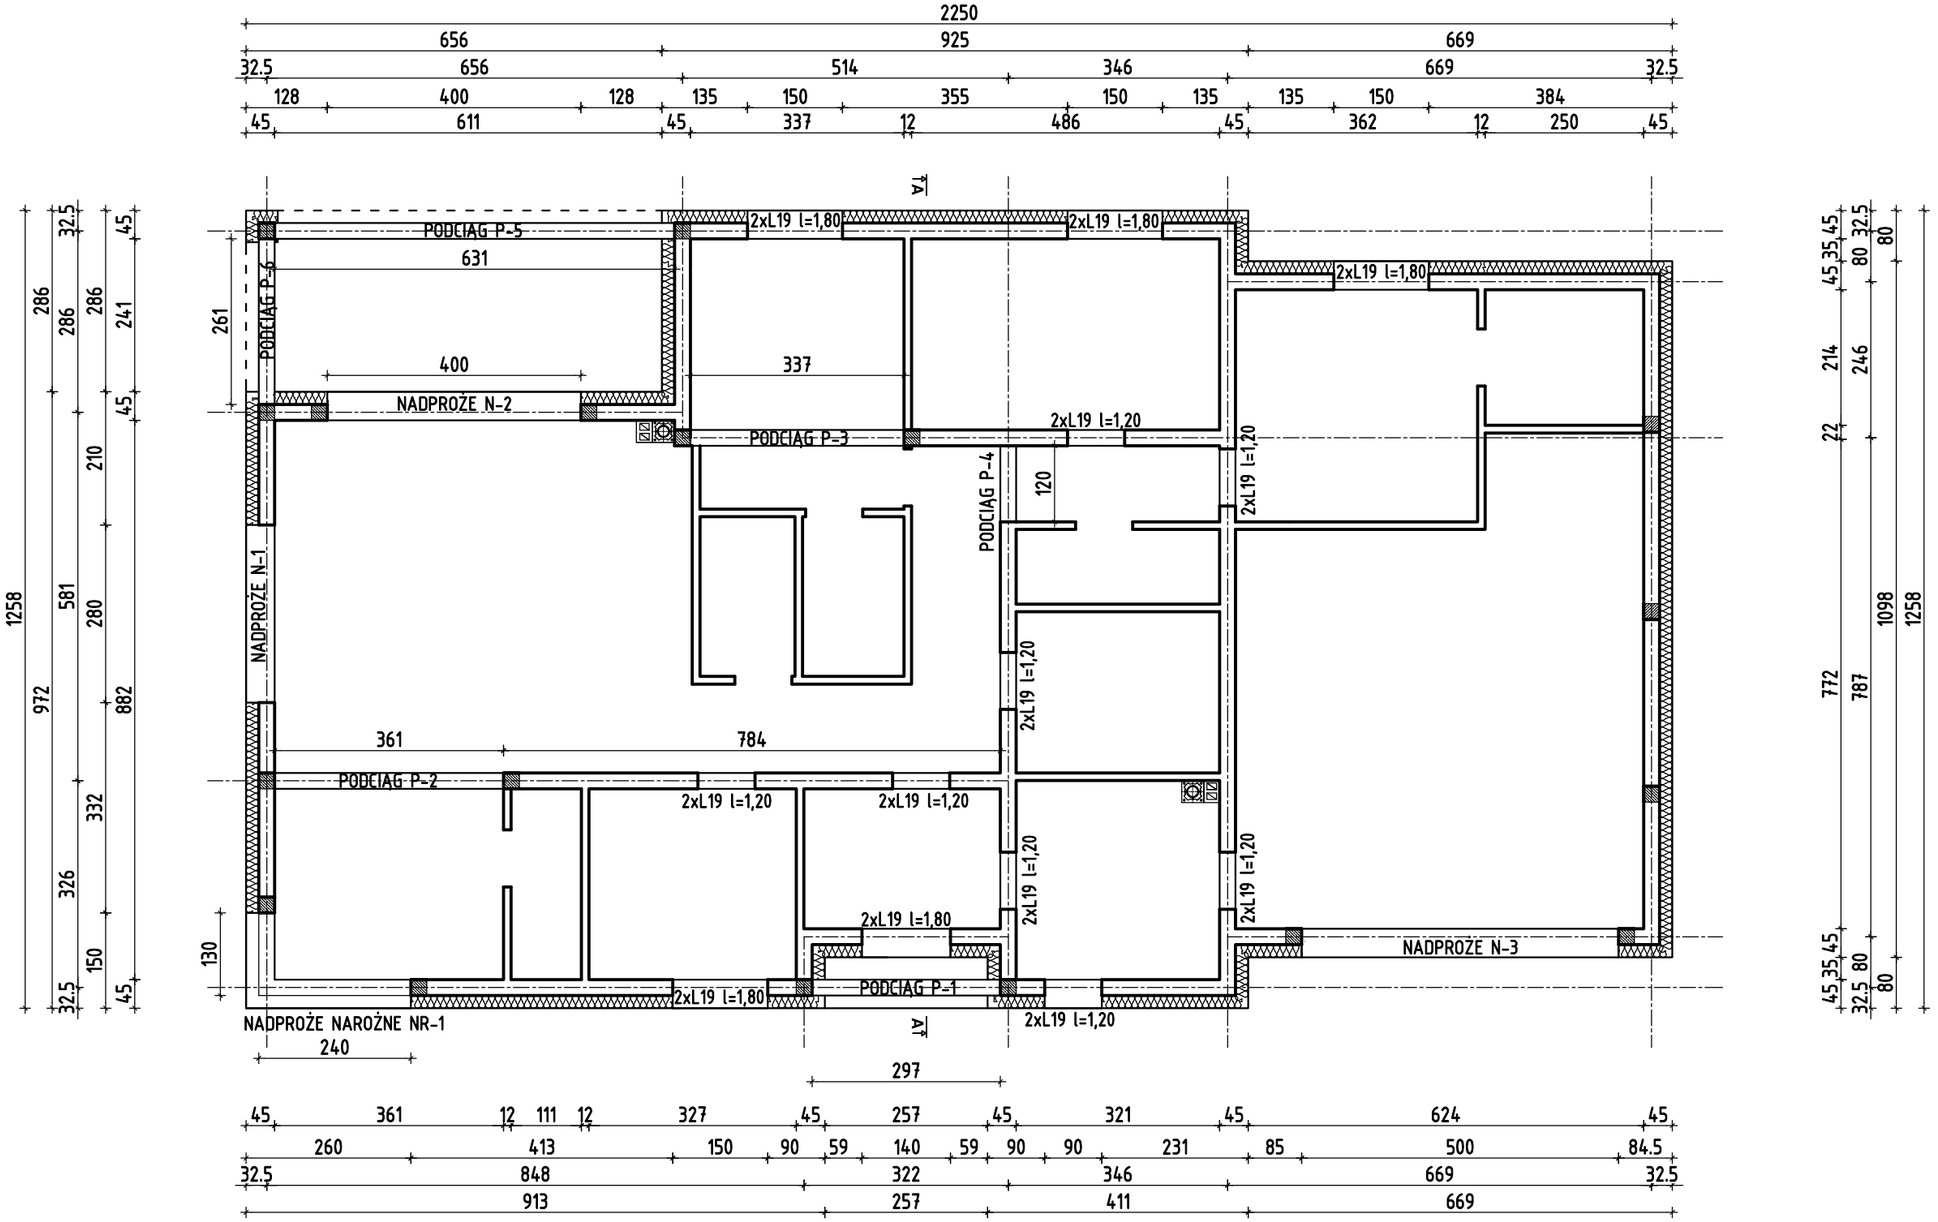


| | | |
|---|---|---|
| *JEDNOSTKA OPRACOWUJĄCA:* TE-DE SP.ZO.O. ul. Nowy Świat 33/13; 00-029 Warszawa; tel. 605 255 383; NIP 5252891372; mail: drozdzielpiotr@gmail.com | | PT |
| INWESTOR: DOMINIK I MARTA GRELA UL. PIŁSUDSKIEGO 15A 23-400 BIŁGORAJ | NAZWA I ADRES OBIEKTU: BUDOWA BUDYNKU MIESZKALNEGO JEDNORODZINNEGO WRAZ Z WEWNĘTRZNĄ INSTALACJĄ ELEKTRYCZNĄ, WODNĄ, KANALIZACJI SANITARNEJ, WENTYLACJI MECHANICZNEJ ORAZ ZEWNĘTRZNĄ INSTALACJĄ KABLOWĄ ELEKTROENERGETYCZNĄ NN ZALICZNIKOWĄ, INSTALACJĄ WODOCIĄGOWĄ I KANALIZACYJNĄ dz. nr 95/9, AR_12; obręb ewidencyjny: 0001 BIŁGORAJ jednostka ewidencyjna: 060201_1 BIŁGORAJ miasto | |
| TYTUŁ RYSUNKU | RZUT KONSRUKCYJNY PARTERU | SKALA 1:100 |
| FUNKCJA | IMIĘ I NAZWISKO ORAZ ZAKRES I SPECJALNOŚĆ UPRAWNIEŃ | PODPIS |
| PROJEKTANT KONSTRUKCJA | mgr inż. Piotr Droździel *upr. bud. do projektowania i kierowania robotami bez ograniczeń w specj. konstrukcyjno – budowlanej LUB/0364/PWBKb/15* | DATA 12.2025 |
| | | NR RYS. 5 |

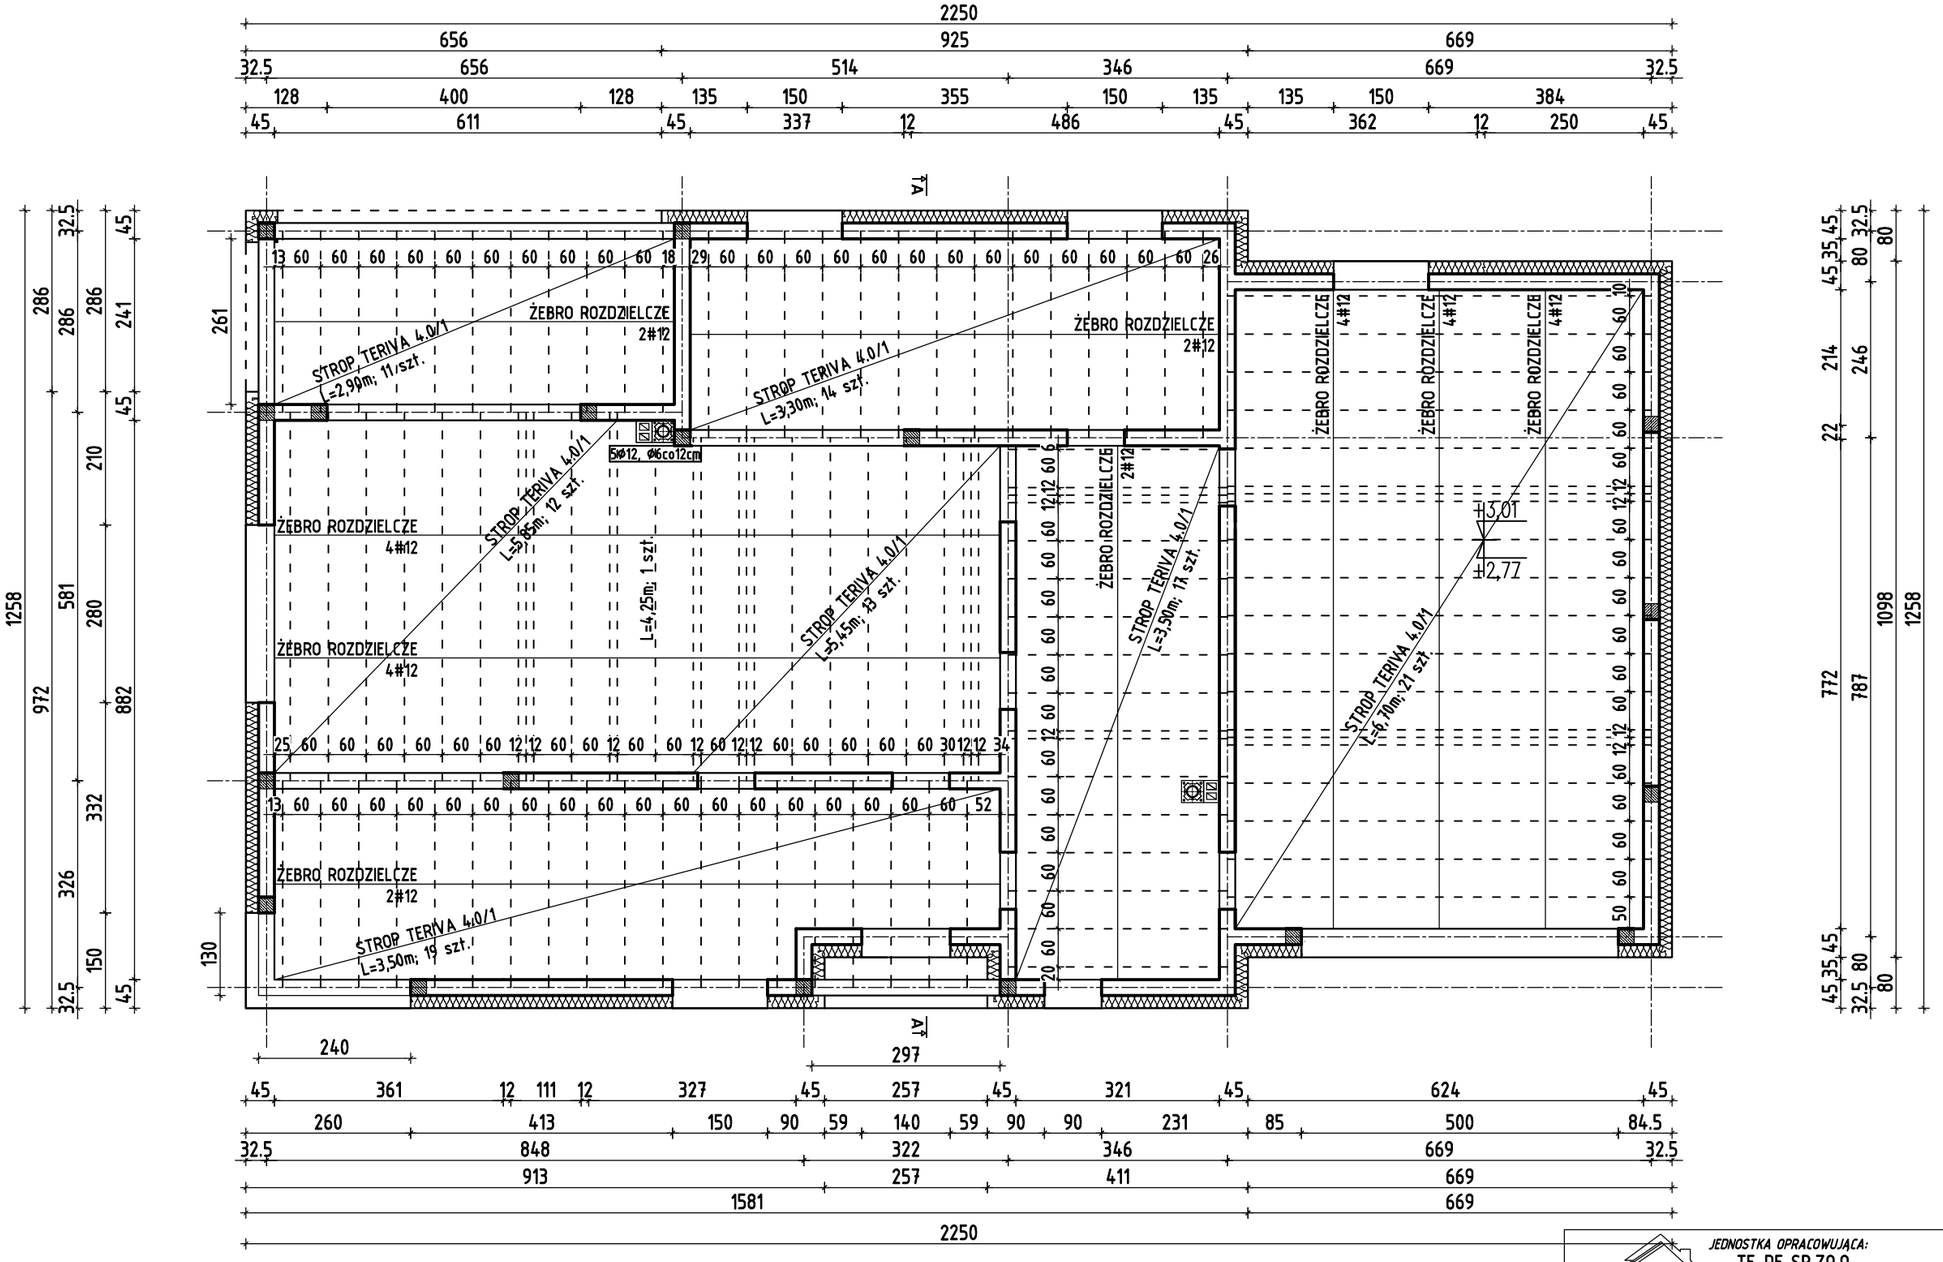



Beton
Stal zbrojeniowa
Stal strzemion
Otulina


| | | |
|---|---|---|
| *JEDNOSTKA OPRACOWUJĄCA:* TE-DE SP.ZO.O. ul. Nowy Świat 33/13; 00–029 Warszawa; tel. 605 255 383; NIP 5252891372; mail: drozdzielpiotr@gmail.com | | PT |
| INWESTOR: DOMINIK I MARTA GRELA UL. PIŁSUDSKIEGO 15A 23–400 BIŁGORAJ | NAZWA I ADRES OBIEKTU: BUDOWA BUDYNKU MIESZKALNEGO JEDNORODZINNEGO WRAZ Z WEWNĘTRZNĄ INSTALACJĄ ELEKTRYCZNĄ, WODNĄ, KANALIZACJI SANITARNEJ, WENTYLACJI MECHANICZNEJ ORAZ ZEWNĘTRZNĄ INSTALACJĄ KABLOWĄ ELEKTROENERGETYCZNĄ NN ZALICZNIKOWĄ, INSTALACJĄ WODOCIĄGOWĄ I KANALIZACYJNĄ dz. nr 95/9, AR_12; obręb ewidencyjny: 0001 BIŁGORAJ jednostka ewidencyjna: 060201_1 BIŁGORAJ miasto | |
| TYTUŁ RYSUNKU | STROP NAD PARTEREM | SKALA 1:100 |
| FUNKCJA | IMIĘ I NAZWISKO ORAZ ZAKRES I SPECJALNOŚĆ UPRAWNIEŃ / PODPIS | |
| PROJEKTANT KONSTRUKCJA | mgr inż. Piotr Droździel *upr. bud. do projektowania i kierowania robotami bez ograniczeń w specj. konstrukcyjno – budowlanej LUB/0364/PWBKb/15* | DATA 12.2025 |
| | | NR RYS. 6 |

# SZCZEGÓŁY STROPU
SKALA 1:20


*WIENIEC W–1*

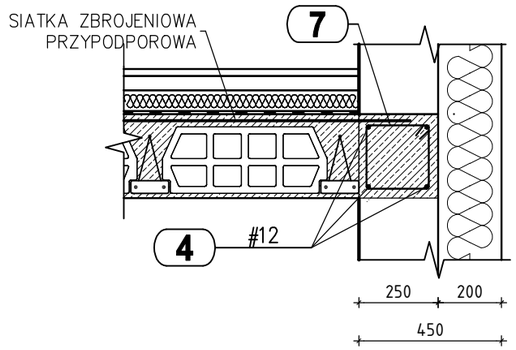



*POZ. 2*

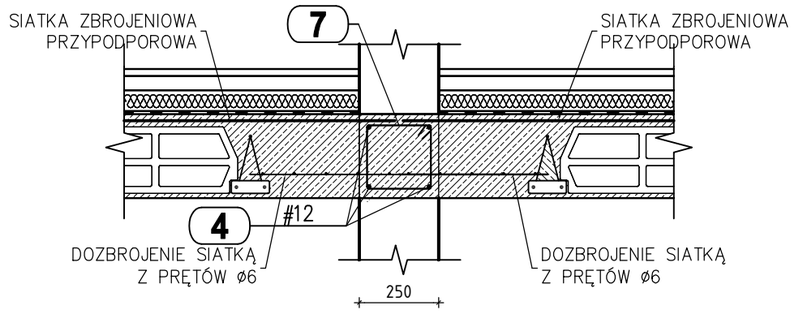




*WIENIEC W–2*

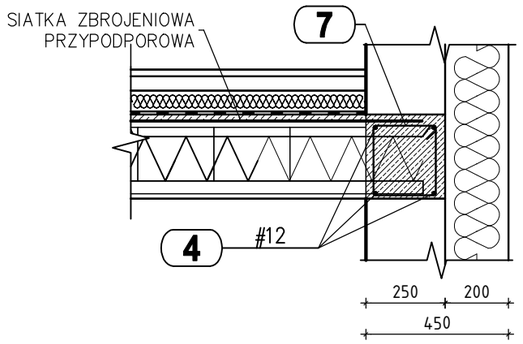



*POZ. 3*

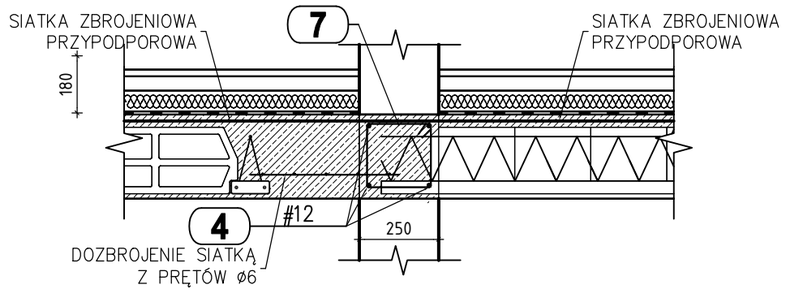

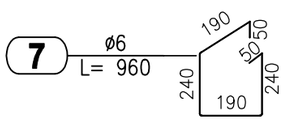
UWAGI:
1. Otulina min. 2,5cm.
2. Min zakład dla prętów:
#12 – 50cm
#16 – 65cm
3. Rozpatrywać łącznie z dokumentacją architektoniczną
4. Przy rozpiętości 7,0m zastosować dodatkowe zbrojenie przypodporowe z siatki ø8
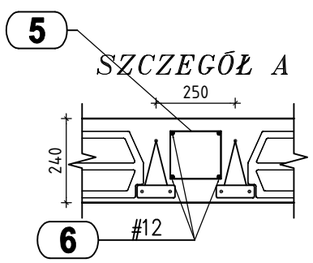
| | |
|---|---|
| Beton | C20/25 (B25) |
| Stal zbrojeniowa | A-IIIN (RB500W) |
| Otulina | 2.5cm |

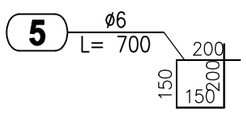
JEDNOSTKA OPRACOWUJĄCA:
TE-DE SP.ZO.O.
ul. Nowy Świat 33/13; 00–029 Warszawa; tel. 605 255 383;
NIP 5252891372; mail: drozdzielpiotr@gmail.com


PT


INWESTOR:
DOMINIK I MARTA GRELA
UL. PIŁSUDSKIEGO 15A
23–400 BIŁGORAJ

NAZWA I ADRES OBIEKTU:
BUDOWA BUDYNKU MIESZKALNEGO JEDNORODZINNEGO WRAZ Z WEWNĘTRZNĄ INSTALACJĄ ELEKTRYCZNĄ, WODNĄ, KANALIZACJI SANITARNEJ, WENTYLACJI MECHANICZNEJ ORAZ ZEWNĘTRZNĄ INSTALACJĄ KABLOWĄ ELEKTROENERGETYCZNĄ NN ZALICZNIKOWĄ, INSTALACJĄ WODOCIĄGOWĄ I KANALIZACYJNĄ
dz. nr 95/9, AR_12; obręb ewidencyjny: 0001 BIŁGORAJ
jednostka ewidencyjna: 060201_1 BIŁGORAJ miasto


| TYTUŁ RYSUNKU | SZCZEGÓŁY STROPU | SKALA 1:20 |
|---|---|---|


| FUNKCJA | IMIĘ I NAZWISKO ORAZ ZAKRES I SPECJALNOŚĆ UPRAWNIEŃ | PODPIS | DATA 12.2025 |
|---|---|---|---|
| PROJEKTANT KONSTRUKCJA | mgr inż. Piotr Droździel<br>*upr. bud. do projektowania i kierowania robotami bez ograniczeń w specj. konstrukcyjno – budowlanej LUB/0364/PWBKb/15* | | |
| | | | NR RYS. 7 |

# TRZPIEŃ T-1
szt. 17

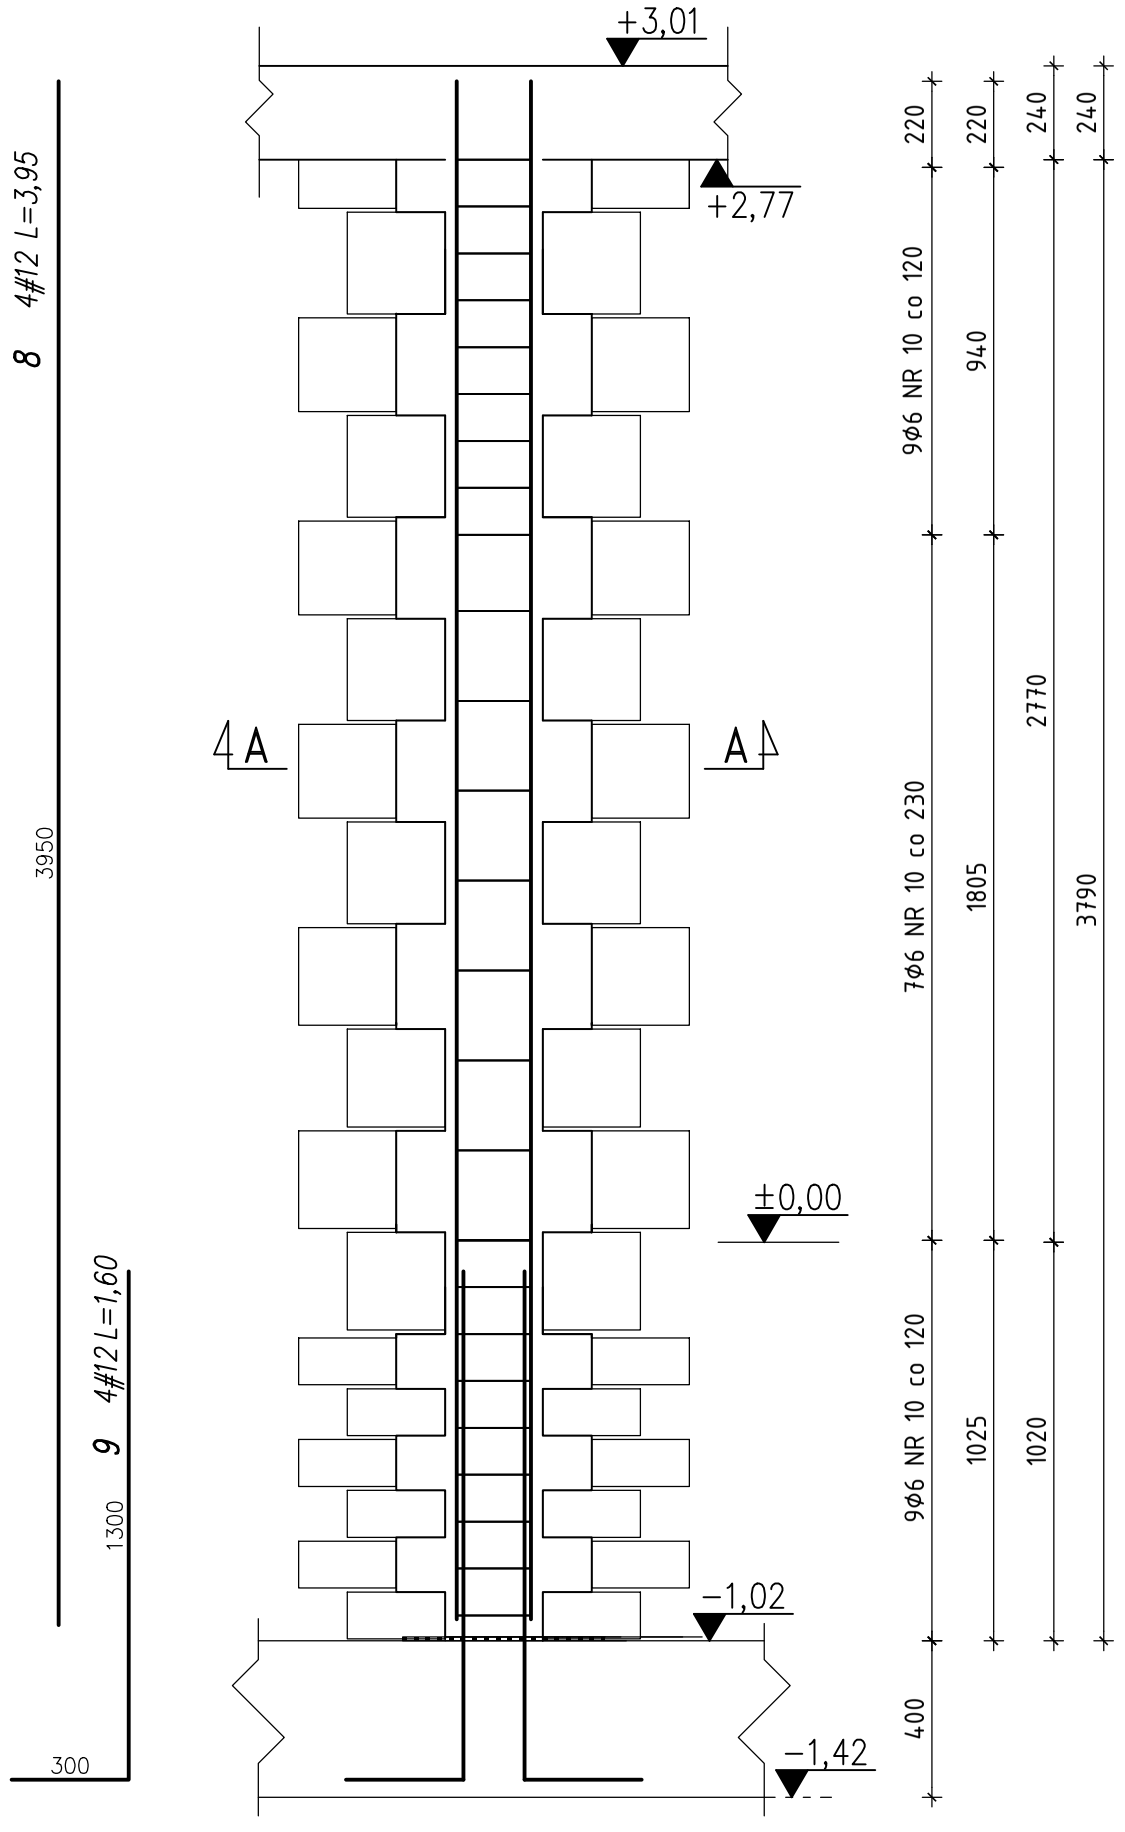


A–A

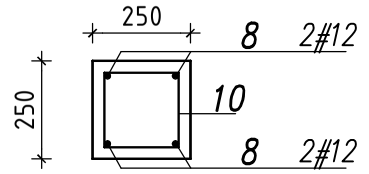

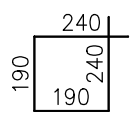
10 26ø6 L=0,86

UWAGA:
1. WYSOKOŚĆ TRZPIENI MIERZONA DO WIEŃCA.
2. WYSOKOŚĆ TRZPIENI ZWERYFIKOWAĆ NA BUDOWIE.

| | |
|---|---|
| Beton | C20/25 (B25) |
| Stal zbrojeniowa | A–IIIN (RB500W) |
| Stal strzemion | A–0 (St–0) |
| Otulina | 2.5cm |


JEDNOSTKA OPRACOWUJĄCA:
TE-DE SP.ZO.O.
ul. Nowy Świat 33/13; 00–029 Warszawa; tel. 605 255 383;
NIP 5252891372; mail: drozdzielpiotr@gmail.com



PT


INWESTOR:
DOMINIK I MARTA GRELA
UL. PIŁSUDSKIEGO 15A
23–400 BIŁGORAJ

NAZWA I ADRES OBIEKTU:
BUDOWA BUDYNKU MIESZKALNEGO JEDNORODZINNEGO WRAZ Z WEWNĘTRZNĄ INSTALACJĄ ELEKTRYCZNĄ, WODNĄ, KANALIZACJI SANITARNEJ, WENTYLACJI MECHANICZNEJ ORAZ ZEWNĘTRZNĄ INSTALACJĄ KABLOWĄ ELEKTROENERGETYCZNĄ NN ZALICZNIKOWĄ, INSTALACJĄ WODOCIĄGOWĄ I KANALIZACYJNĄ
dz. nr 95/9, AR_12; obręb ewidencyjny: 0001 BIŁGORAJ
jednostka ewidencyjna: 060201_1 BIŁGORAJ miasto

| | | |
|---|---|---|
| TYTUŁ RYSUNKU | TRZPIEŃ T-1 | SKALA 1:20 |
| FUNKCJA | IMIĘ I NAZWISKO ORAZ ZAKRES I SPECJALNOŚĆ UPRAWNIEŃ / PODPIS | |
| PROJEKTANT KONSTRUKCJA | mgr inż. Piotr Droździel<br>*upr. bud. do projektowania i kierowania robotami bez ograniczeń w specj. konstrukcyjno – budowlanej LUB/0364/PWBKb/15* | DATA 12.2025 |
| | | NR RYS. 8 |

# SŁUP S-1
szt. 1

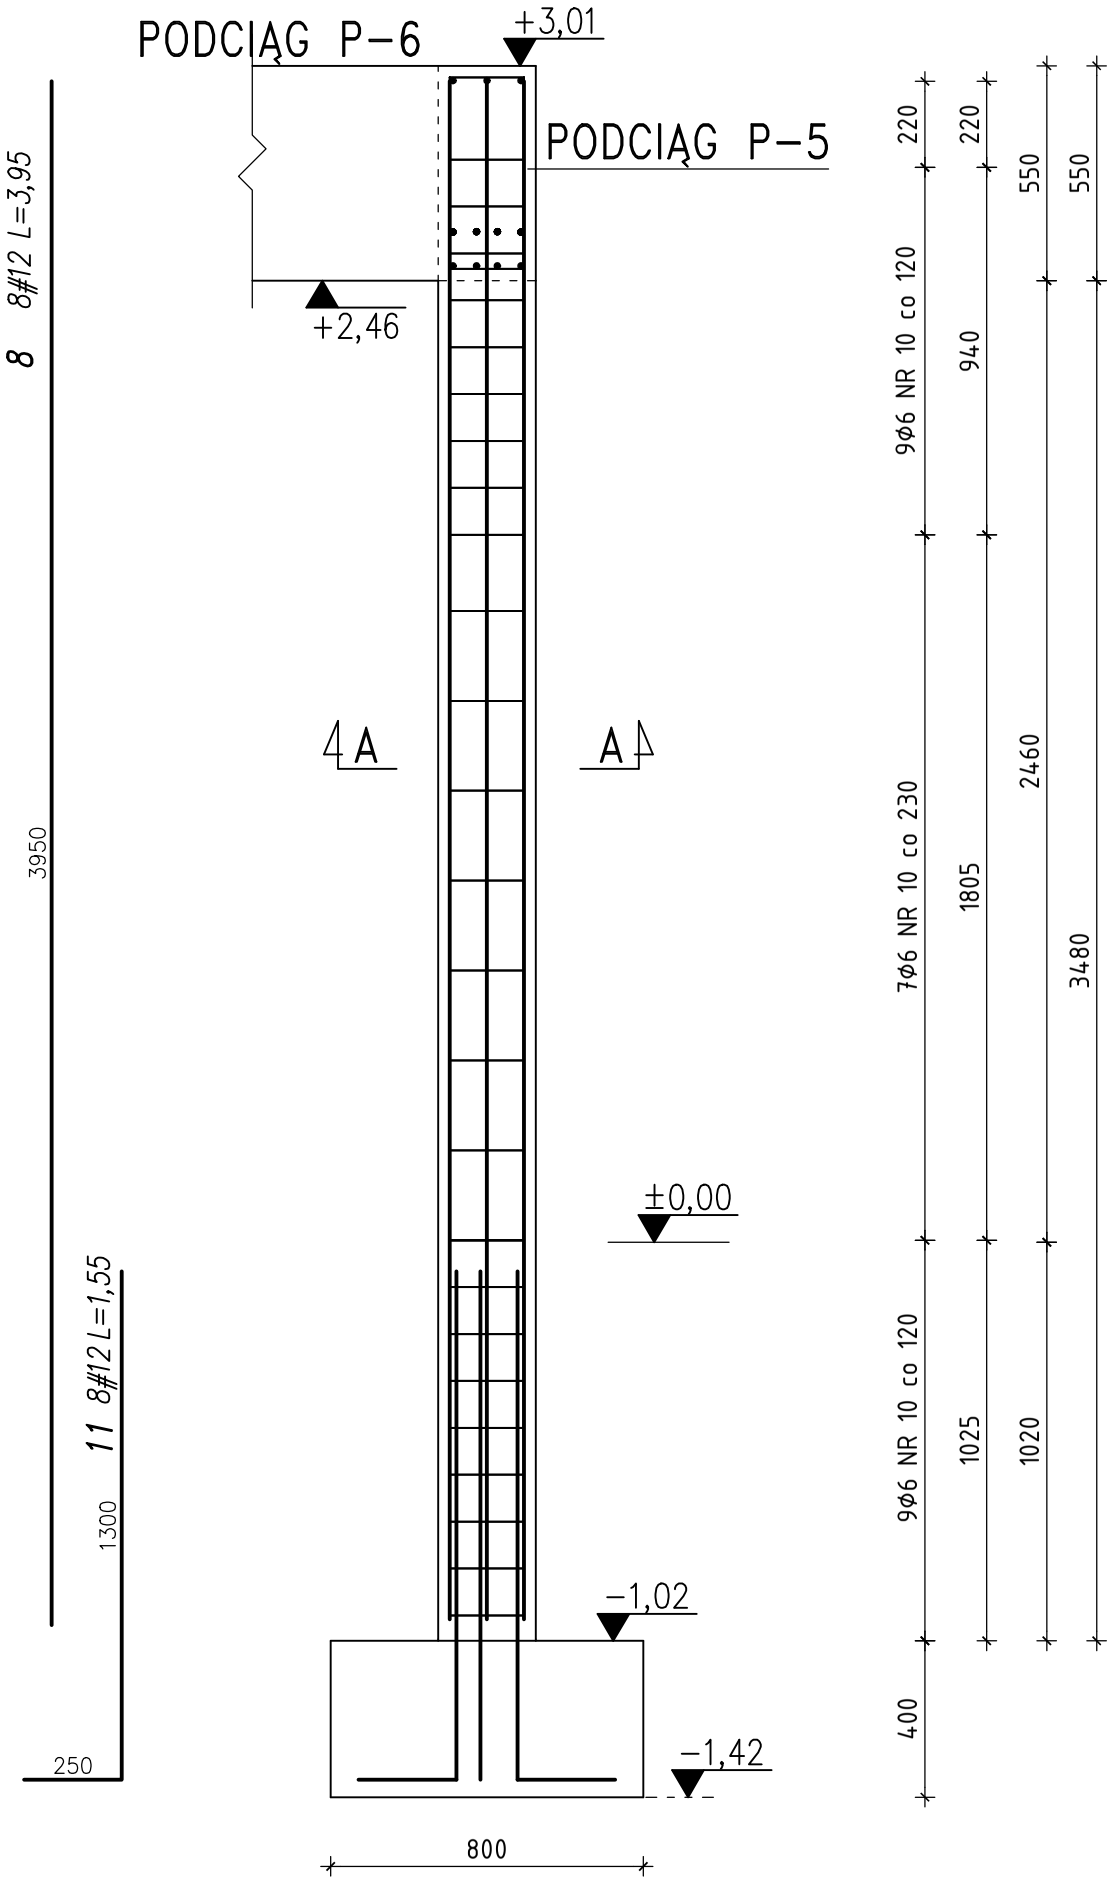

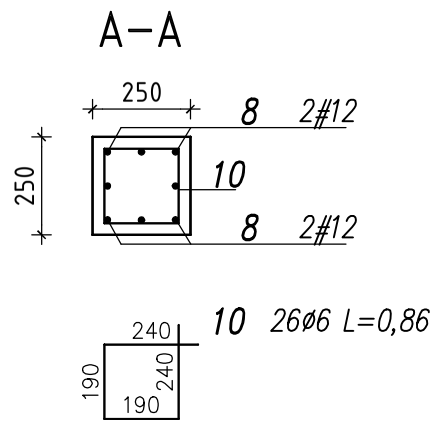
UWAGA:
1. WYSOKOŚĆ SŁUPA MIERZONA DO PODCIĄGU.
2. WYSOKOŚĆ SŁUPA ZWERYFIKOWAĆ NA BUDOWIE.

| | |
|---|---|
| Beton | C20/25 (B25) |
| Stal zbrojeniowa | A-IIIN (RB500W) |
| Stal strzemion | A-0 (St-0) |
| Otulina | 2.5cm |


JEDNOSTKA OPRACOWUJĄCA:
TE-DE SP.Z O.O.
ul. Nowy Świat 33/13; 00-029 Warszawa; tel. 605 255 383;
NIP 5252891372; mail: drozdzielpiotr@gmail.com


PT

INWESTOR:
DOMINIK I MARTA GRELA
UL. PIŁSUDSKIEGO 15A
23-400 BIŁGORAJ


NAZWA I ADRES OBIEKTU:
BUDOWA BUDYNKU MIESZKALNEGO JEDNORODZINNEGO WRAZ Z WEWNĘTRZNĄ INSTALACJĄ ELEKTRYCZNĄ, WODNĄ, KANALIZACJI SANITARNEJ, WENTYLACJI MECHANICZNEJ ORAZ ZEWNĘTRZNĄ INSTALACJĄ KABLOWĄ ELEKTROENERGETYCZNĄ NN ZALICZNIKOWĄ, INSTALACJĄ WODOCIĄGOWĄ I KANALIZACYJNĄ
dz. nr 95/9, AR_12; obręb ewidencyjny: 0001 BIŁGORAJ
jednostka ewidencyjna: 060201_1 BIŁGORAJ miasto


| TYTUŁ RYSUNKU | SŁUP S-1 | | SKALA 1:20 |
|---|---|---|---|
| FUNKCJA | IMIĘ I NAZWISKO ORAZ ZAKRES I SPECJALNOŚĆ UPRAWNIEŃ | PODPIS | |
| PROJEKTANT KONSTRUKCJA | mgr inż. Piotr Droździel<br>*upr. bud. do projektowania i kierowania robotami bez ograniczeń w specj. konstrukcyjno – budowlanej LUB/0364/PWBKb/15* | | DATA 12.2025 |
| | | | NR RYS. 9 |


# NADPROŻE NAROŻNE NR-1

SKALA 1:20


szt. 1

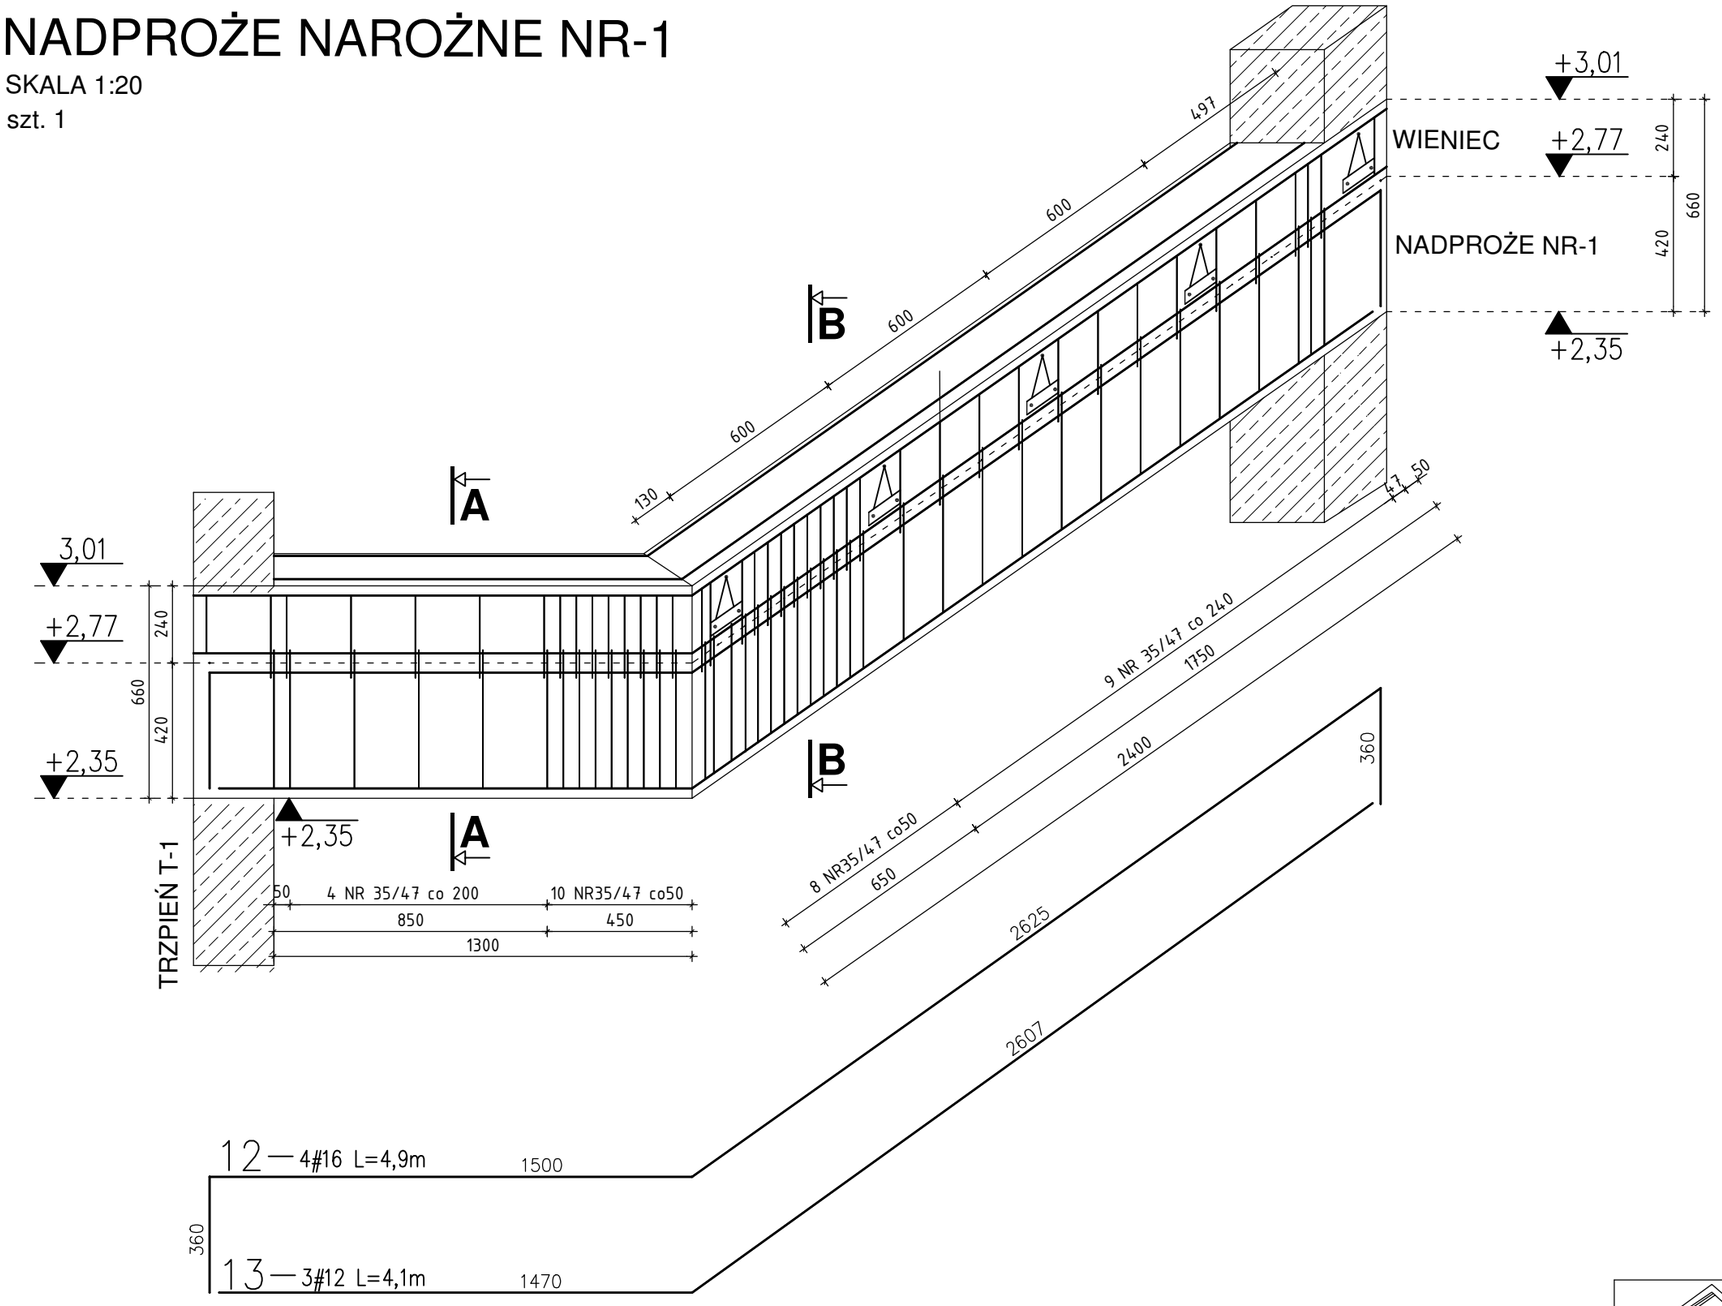

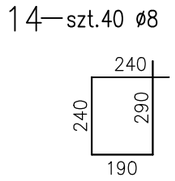


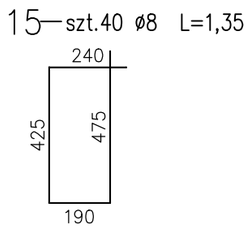

## A-A

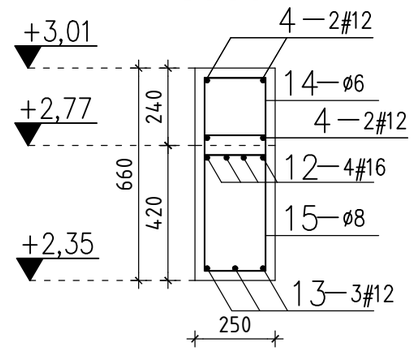


## B-B

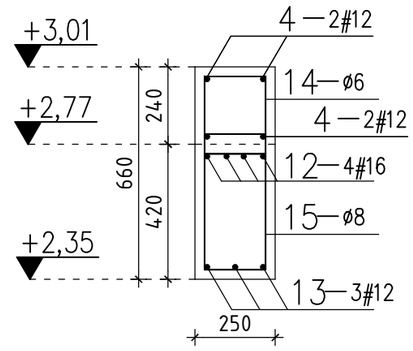


| | |
|---|---|
| Beton | C20/25 (B25) |
| Stal zbrojeniowa | A-IIIN (RB500W) |
| Stal strzemion | A-I |
| Otulina | 2.5cm |

**UWAGA:**

1. NADPROŻE NAROŻNE NR-1 POŁACZONE Z WIEŃCEM.


JEDNOSTKA OPRACOWUJĄCA:
TE-DE SP.Z O.O.
ul. Nowy Świat 33/13; 00-029 Warszawa; tel. 605 255 383;
NIP 5252891372; mail: drozdzielpiotr@gmail.com


PT

INWESTOR:
DOMINIK I MARTA GRELA
UL. PIŁSUDSKIEGO 15A
23-400 BIŁGORAJ

NAZWA I ADRES OBIEKTU:
BUDOWA BUDYNKU MIESZKALNEGO JEDNORODZINNEGO WRAZ Z WEWNĘTRZNĄ INSTALACJĄ ELEKTRYCZNĄ, WODNĄ, KANALIZACJI SANITARNEJ, WENTYLACJI MECHANICZNEJ ORAZ ZEWNĘTRZNĄ INSTALACJĄ KABLOWĄ ELEKTROENERGETYCZNĄ NN ZALICZNIKOWĄ, INSTALACJĄ WODOCIĄGOWĄ I KANALIZACYJNĄ
dz. nr 95/9, AR_12; obręb ewidencyjny: 0001 BIŁGORAJ
jednostka ewidencyjna: 060201_1 BIŁGORAJ miasto


| TYTUŁ RYSUNKU | NADPROŻE NAROŻNE NR-1 | SKALA 1: 20 |
|---|---|---|


| FUNKCJA | IMIĘ I NAZWISKO ORAZ ZAKRES I SPECJALNOŚĆ UPRAWNIEŃ | PODPIS | |
|---|---|---|---|
| PROJEKTANT KONSTRUKCJA | mgr inż. Piotr Droździel<br>*upr. bud. do projektowania i kierowania robotami bez ograniczeń w specj. konstrukcyjno – budowlanej LUB/0364/PWBKb/15* | | DATA 12.2025 |
| | | | NR RYS. 10 |

# NADPROŻE N-1


SKALA 1:20

SZT. 1

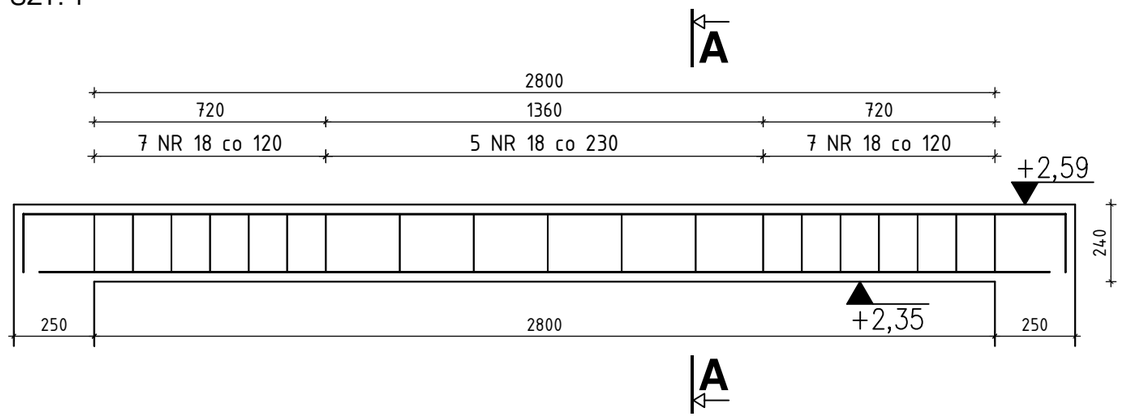


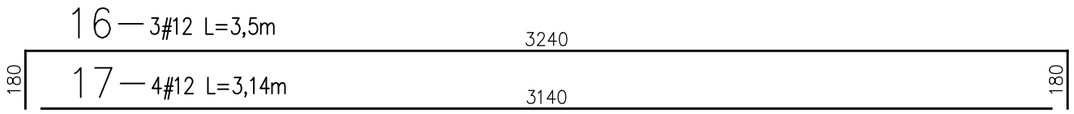
## A-A

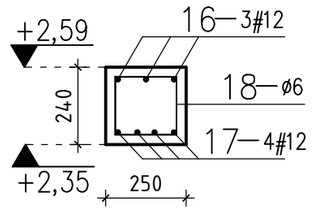


18 — szt.19 ø6 L=0,85

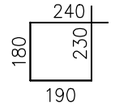


| | |
|---|---|
| Beton | C20/25 (B25) |
| Stal zbrojeniowa | A-IIIN (RB500W) |
| Stal strzemion | A-I |
| Otulina | 2.5cm |


JEDNOSTKA OPRACOWUJĄCA:
TE-DE SP.ZO.O.
ul. Nowy Świat 33/13; 00-029 Warszawa; tel. 605 255 383;
NIP 5252891372; mail: drozdzielpiotr@gmail.com


PT

INWESTOR:
DOMINIK I MARTA GRELA
UL. PIŁSUDSKIEGO 15A
23-400 BIŁGORAJ


NAZWA I ADRES OBIEKTU:
BUDOWA BUDYNKU MIESZKALNEGO JEDNORODZINNEGO WRAZ Z WEWNĘTRZNĄ INSTALACJĄ ELEKTRYCZNĄ, WODNĄ, KANALIZACJI SANITARNEJ, WENTYLACJI MECHANICZNEJ ORAZ ZEWNĘTRZNĄ INSTALACJĄ KABLOWĄ ELEKTROENERGETYCZNĄ NN ZALICZNIKOWĄ, INSTALACJĄ WODOCIĄGOWĄ I KANALIZACYJNĄ
dz. nr 95/9, AR_12; obręb ewidencyjny: 0001 BIŁGORAJ
jednostka ewidencyjna: 060201_1 BIŁGORAJ miasto


| TYTUŁ RYSUNKU | NADPROŻE N-1 | SKALA 1: 20 |
|---|---|---|
| FUNKCJA | IMIĘ I NAZWISKO ORAZ ZAKRES I SPECJALNOŚĆ UPRAWNIEŃ | PODPIS |
| PROJEKTANT KONSTRUKCJA | mgr inż. Piotr Droździel<br>*upr. bud. do projektowania i kierowania robotami bez ograniczeń w specj. konstrukcyjno – budowlanej LUB/0364/PWBKb/15* | DATA 12.2025 |
| | | NR RYS. 11 |


# NADPROŻE N-2


SKALA 1:20


SZT. 1

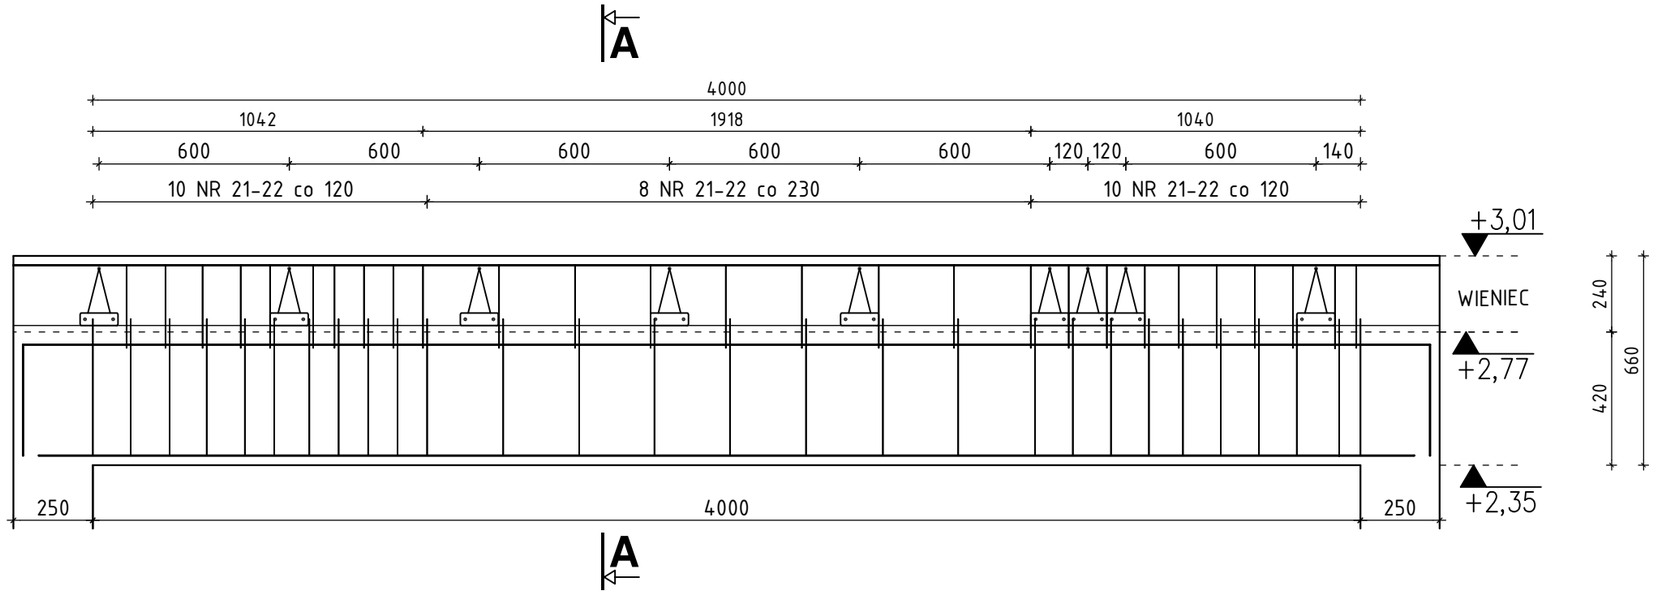

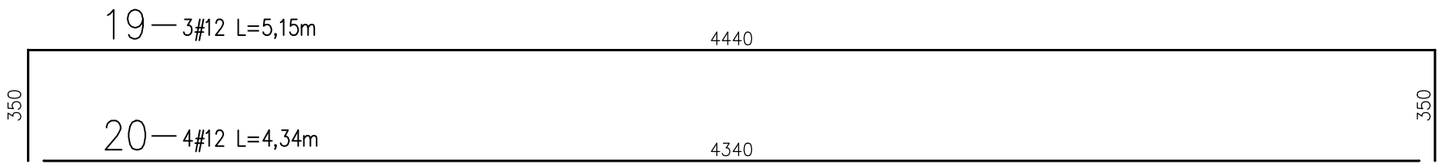
| | |
|---|---|
| Beton | C20/25 (B25) |
| Stal zbrojeniowa | A–IIIN (RB500W) |
| Stal strzemion | A–0 (St–0) |
| Otulina | 2.5cm |

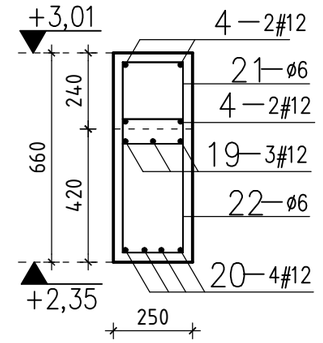UWAGA:

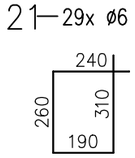1. NADPROŻE N–2 POŁĄCZONE Z WIEŃCEM.

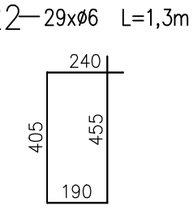
JEDNOSTKA OPRACOWUJĄCA:
TE-DE SP.ZO.O.
ul. Nowy Świat 33/13; 00–029 Warszawa; tel. 605 255 383;
NIP 5252891372; mail: drozdzielpiotr@gmail.com


PT

INWESTOR:
DOMINIK I MARTA GRELA
UL. PIŁSUDSKIEGO 15A
23–400 BIŁGORAJ


NAZWA I ADRES OBIEKTU:
BUDOWA BUDYNKU MIESZKALNEGO JEDNORODZINNEGO WRAZ Z WEWNĘTRZNĄ INSTALACJĄ ELEKTRYCZNĄ, WODNĄ, KANALIZACJI SANITARNEJ, WENTYLACJI MECHANICZNEJ ORAZ ZEWNĘTRZNĄ INSTALACJĄ KABLOWĄ ELEKTROENERGETYCZNĄ NN ZALICZNIKOWĄ, INSTALACJĄ WODOCIĄGOWĄ I KANALIZACYJNĄ
dz. nr 95/9, AR_12; obręb ewidencyjny: 0001 BIŁGORAJ
jednostka ewidencyjna: 060201_1 BIŁGORAJ miasto


| | | |
|---|---|---|
| TYTUŁ RYSUNKU | NADPROŻE N-2 | SKALA 1:20 |
| FUNKCJA | IMIĘ I NAZWISKO ORAZ ZAKRES I SPECJALNOŚĆ UPRAWNIEŃ | PODPIS |
| PROJEKTANT KONSTRUKCJA | mgr inż. Piotr Droździel<br>*upr. bud. do projektowania i kierowania robotami bez ograniczeń w specj. konstrukcyjno – budowlanej LUB/0364/PWBKb/15* | DATA 12.2025 |
| | | NR RYS. 12 |

# NADPROŻE N-3


SKALA 1:20


SZT. 1

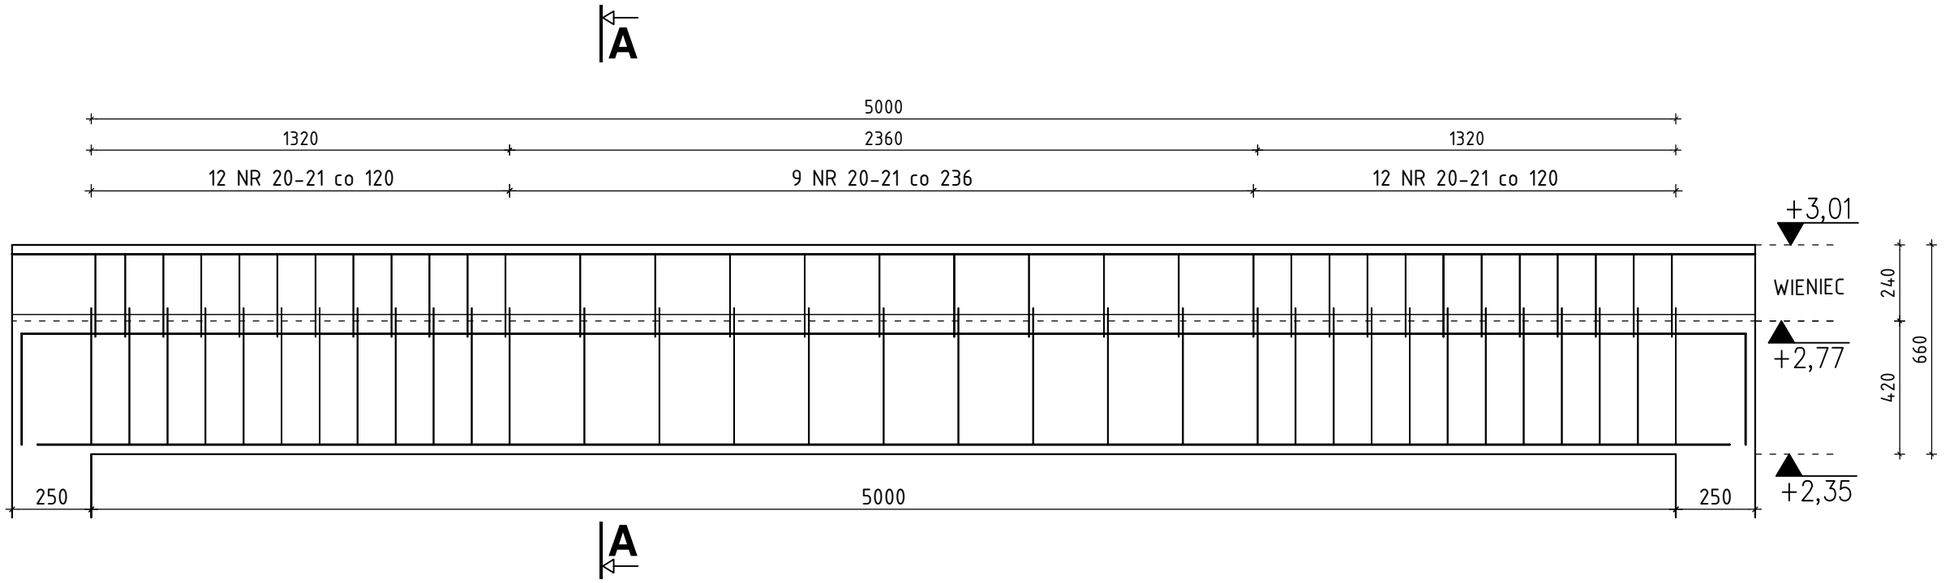

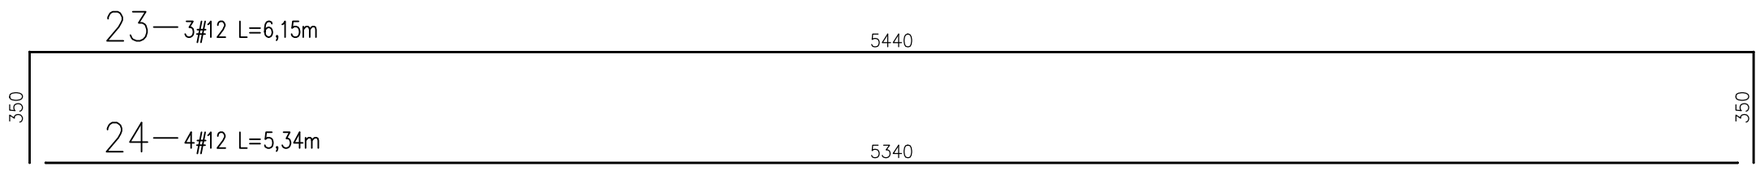
## A-A

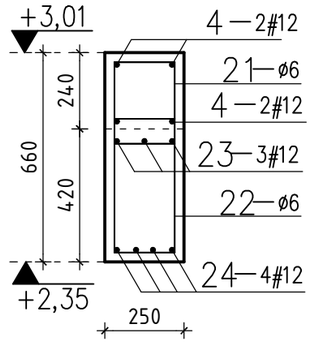


| | |
|---|---|
| Beton | C20/25 (B25) |
| Stal zbrojeniowa | A–IIIN (RB500W) |
| Stal strzemion | A–0 (St–0) |
| Otulina | 2.5cm |

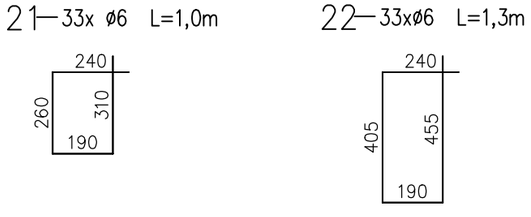UWAGA:

1. NADPROŻE N–3 POŁĄCZONE Z WIEŃCEM.


JEDNOSTKA OPRACOWUJĄCA:
TE-DE SP.ZO.O.
ul. Nowy Świat 33/13; 00–029 Warszawa; tel. 605 255 383;
NIP 5252891372; mail: drozdzielpiotr@gmail.com


PT

INWESTOR:
DOMINIK I MARTA GRELA
UL. PIŁSUDSKIEGO 15A
23–400 BIŁGORAJ


NAZWA I ADRES OBIEKTU:
BUDOWA BUDYNKU MIESZKALNEGO JEDNORODZINNEGO WRAZ Z WEWNĘTRZNĄ INSTALACJĄ ELEKTRYCZNĄ, WODNĄ, KANALIZACJI SANITARNEJ, WENTYLACJI MECHANICZNEJ ORAZ ZEWNĘTRZNĄ INSTALACJĄ KABLOWĄ ELEKTROENERGETYCZNĄ NN ZALICZNIKOWĄ, INSTALACJĄ WODOCIĄGOWĄ I KANALIZACYJNĄ
dz. nr 95/9, AR_12; obręb ewidencyjny: 0001 BIŁGORAJ
jednostka ewidencyjna: 060201_1 BIŁGORAJ miasto


| TYTUŁ RYSUNKU | NADPROŻE N-3 | SKALA 1:20 |
|---|---|---|
| FUNKCJA | IMIĘ I NAZWISKO ORAZ ZAKRES I SPECJALNOŚĆ UPRAWNIEŃ / PODPIS | |
| PROJEKTANT KONSTRUKCJA | mgr inż. Piotr Droździel<br>*upr. bud. do projektowania i kierowania robotami bez ograniczeń w specj. konstrukcyjno – budowlanej LUB/0364/PWBKb/15* | DATA 12.2025 |
| | | NR RYS. 13 |

# PODCIĄG P-1

SKALA 1:20

SZT. 1

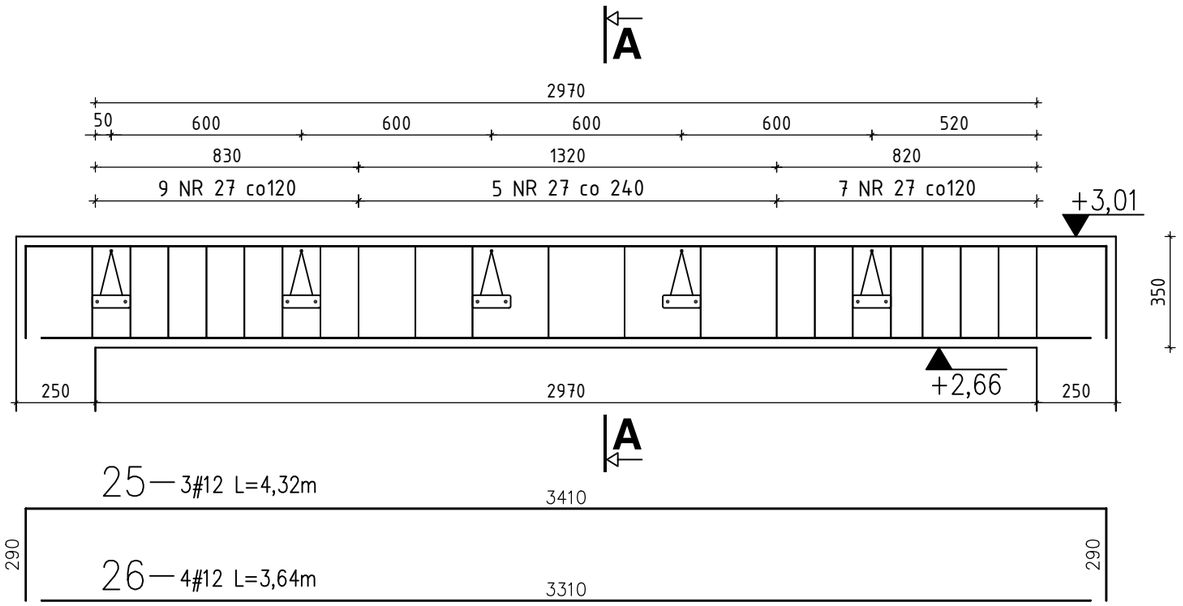

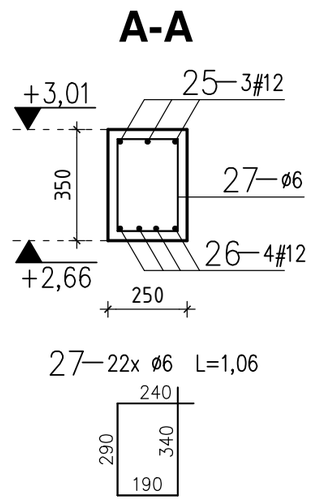



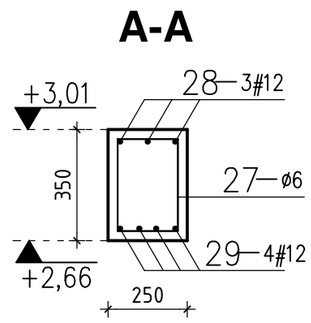

| | |
|---|---|
| Beton | C20/25 (B25) |
| Stal zbrojeniowa | A–IIIN (RB500W) |
| Stal strzemion | A–0 (St–0) |
| Otulina | 2.5cm |

| | | |
|---|---|---|
| *JEDNOSTKA OPRACOWUJĄCA:* **TE-DE SP.Z O.O.** ul. Nowy Świat 33/13; 00–029 Warszawa; tel. 605 255 383; NIP 5252891372; mail: drozdzielpiotr@gmail.com | | PT |
| **INWESTOR:** DOMINIK I MARTA GRELA UL. PIŁSUDSKIEGO 15A 23–400 BIŁGORAJ | **NAZWA I ADRES OBIEKTU:** BUDOWA BUDYNKU MIESZKALNEGO JEDNORODZINNEGO WRAZ Z WEWNĘTRZNĄ INSTALACJĄ ELEKTRYCZNĄ, WODNĄ, KANALIZACJI SANITARNEJ, WENTYLACJI MECHANICZNEJ ORAZ ZEWNĘTRZNĄ INSTALACJĄ KABLOWĄ ELEKTROENERGETYCZNĄ NN ZALICZNIKOWĄ, INSTALACJĄ WODOCIĄGOWĄ I KANALIZACYJNĄ dz. nr 95/9, AR_12; obręb ewidencyjny: 0001 BIŁGORAJ jednostka ewidencyjna: 060201_1 BIŁGORAJ miasto | |
| **TYTUŁ RYSUNKU** | PODCIĄG P-1 | **SKALA** 1: 20 |
| **FUNKCJA** | **IMIĘ I NAZWISKO ORAZ ZAKRES I SPECJALNOŚĆ UPRAWNIEŃ** / **PODPIS** | |
| **PROJEKTANT KONSTRUKCJA** | **mgr inż. Piotr Droździel** *upr. bud. do projektowania i kierowania robotami bez ograniczeń w specj. konstrukcyjno – budowlanej LUB/0364/PWBKb/15* | **DATA** 12.2025 |
| | | **NR RYS.** 14 |


# PODCIĄG P-2

SKALA 1:20
SZT. 1

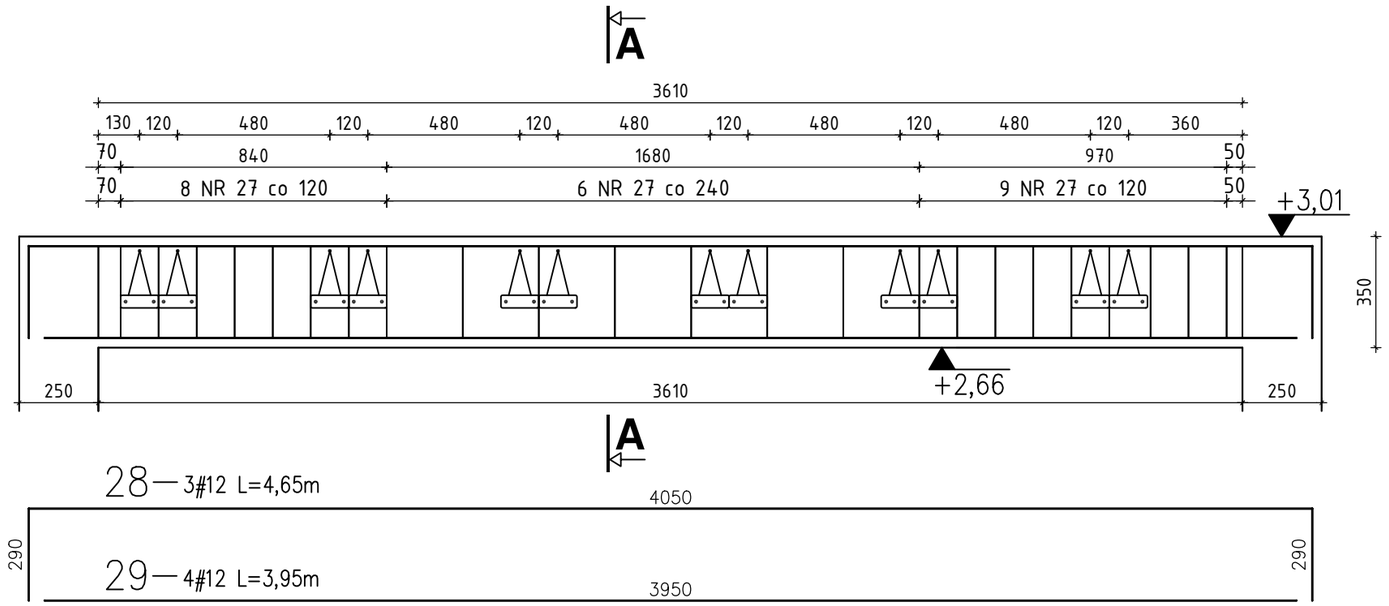


27 — 25x ø6 L=1,06

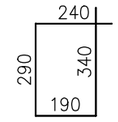


| | |
|---|---|
| Beton | C20/25 (B25) |
| Stal zbrojeniowa | A–IIIN (RB500W) |
| Stal strzemion | A–0 (St–0) |
| Otulina | 2.5cm |


JEDNOSTKA OPRACOWUJĄCA:
TE-DE SP.Z O.O.
ul. Nowy Świat 33/13; 00–029 Warszawa; tel. 605 255 383;
NIP 5252891372; mail: drozdzielpiotr@gmail.com


PT


INWESTOR:
DOMINIK I MARTA GRELA
UL. PIŁSUDSKIEGO 15A
23–400 BIŁGORAJ

NAZWA I ADRES OBIEKTU:
BUDOWA BUDYNKU MIESZKALNEGO JEDNORODZINNEGO WRAZ Z WEWNĘTRZNĄ INSTALACJĄ ELEKTRYCZNĄ, WODNĄ, KANALIZACJI SANITARNEJ, WENTYLACJI MECHANICZNEJ ORAZ ZEWNĘTRZNĄ INSTALACJĄ KABLOWĄ ELEKTROENERGETYCZNĄ NN ZALICZNIKOWĄ, INSTALACJĄ WODOCIĄGOWĄ I KANALIZACYJNĄ
dz. nr 95/9, AR_12; obręb ewidencyjny: 0001 BIŁGORAJ
jednostka ewidencyjna: 060201_1 BIŁGORAJ miasto


| TYTUŁ RYSUNKU | PODCIĄG P-2 | SKALA 1:20 |
|---|---|---|
| FUNKCJA | IMIĘ I NAZWISKO ORAZ ZAKRES I SPECJALNOŚĆ UPRAWNIEŃ | PODPIS |
| PROJEKTANT KONSTRUKCJA | mgr inż. Piotr Droździel<br>*upr. bud. do projektowania i kierowania robotami bez ograniczeń w specj. konstrukcyjno – budowlanej LUB/0364/PWBKb/15* | DATA 12.2025 |
| | | NR RYS. 15 |

# PODCIĄG P-3


SKALA 1:20
SZT. 1

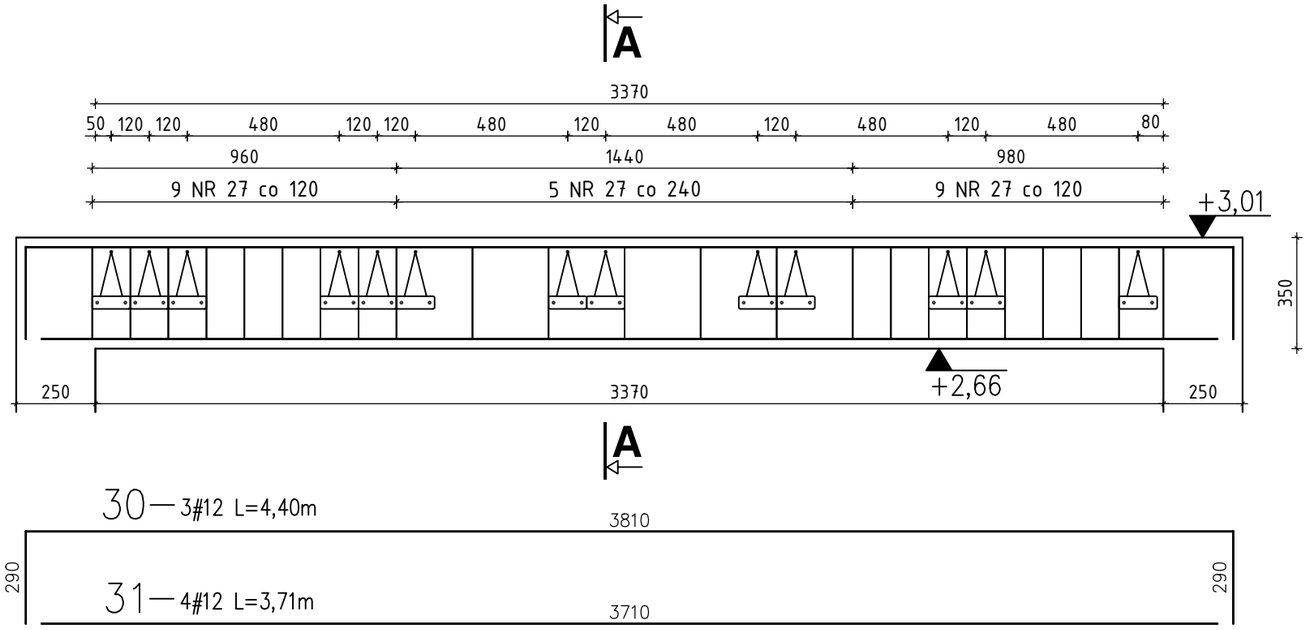


## A-A

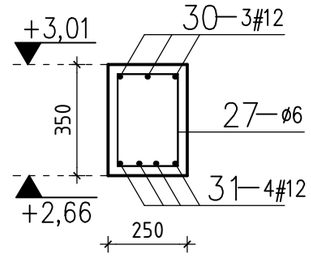



27— 23x ø6 L=1,06

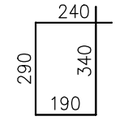



# PODCIĄG P-4


SKALA 1:20
SZT. 1

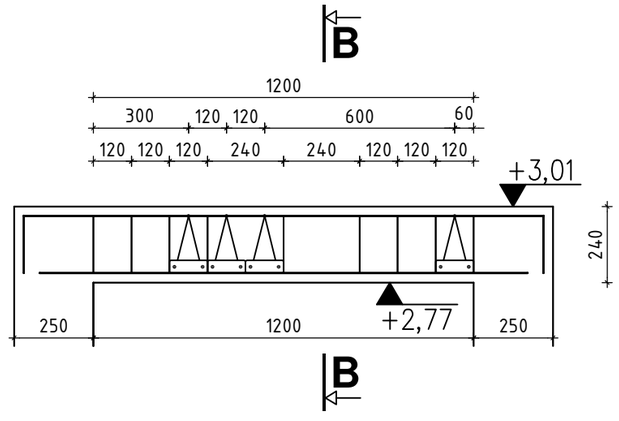


## B-B

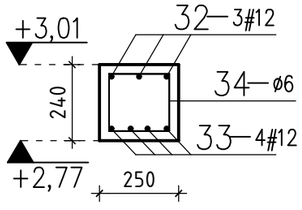



32— 3#12 L=2,00m

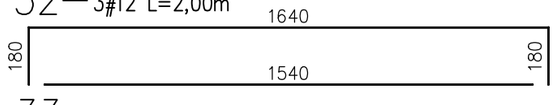


33— 4#12 L=1,54m

34— szt.9 ø6 L=0,85

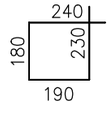


| | |
|---|---|
| Beton | C20/25 (B25) |
| Stal zbrojeniowa | A–IIIN (RB500W) |
| Stal strzemion | A–0 (St–0) |
| Otulina | 2.5cm |


JEDNOSTKA OPRACOWUJĄCA:
TE-DE SP.ZO.O.
ul. Nowy Świat 33/13; 00–029 Warszawa; tel. 605 255 383;
NIP 5252891372; mail: drozdzielpiotr@gmail.com


PT

INWESTOR:
DOMINIK I MARTA GRELA
UL. PIŁSUDSKIEGO 15A
23–400 BIŁGORAJ


NAZWA I ADRES OBIEKTU:
BUDOWA BUDYNKU MIESZKALNEGO JEDNORODZINNEGO WRAZ Z WEWNĘTRZNĄ INSTALACJĄ ELEKTRYCZNĄ, WODNĄ, KANALIZACJI SANITARNEJ, WENTYLACJI MECHANICZNEJ ORAZ ZEWNĘTRZNĄ INSTALACJĄ KABLOWĄ ELEKTROENERGETYCZNĄ NN ZALICZNIKOWĄ, INSTALACJĄ WODOCIĄGOWĄ I KANALIZACYJNĄ
dz. nr 95/9, AR_12; obręb ewidencyjny: 0001 BIŁGORAJ
jednostka ewidencyjna: 060201_1 BIŁGORAJ miasto


| TYTUŁ RYSUNKU | PODCIĄG P-3; PODCIĄG P-4 | SKALA 1: 20 |
|---|---|---|
| FUNKCJA | IMIĘ I NAZWISKO ORAZ ZAKRES I SPECJALNOŚĆ UPRAWNIEŃ | PODPIS |
| PROJEKTANT KONSTRUKCJA | mgr inż. Piotr Droździel<br>*upr. bud. do projektowania i kierowania robotami bez ograniczeń w specj. konstrukcyjno – budowlanej LUB/0364/PWBKb/15* | DATA 12.2025 |
| | | NR RYS. 16 |

# PODCIĄG P-5


SKALA 1:20


SZT. 1

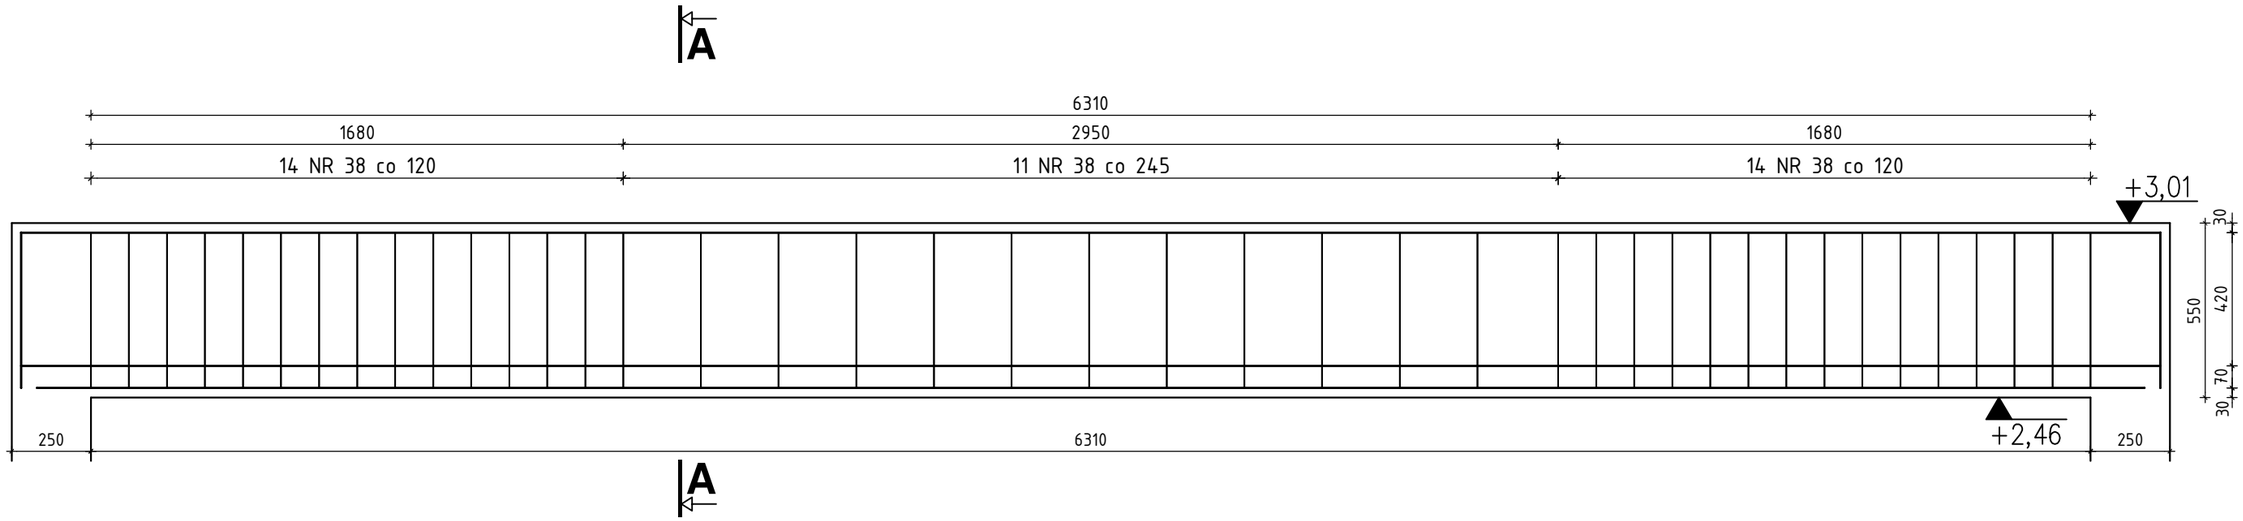

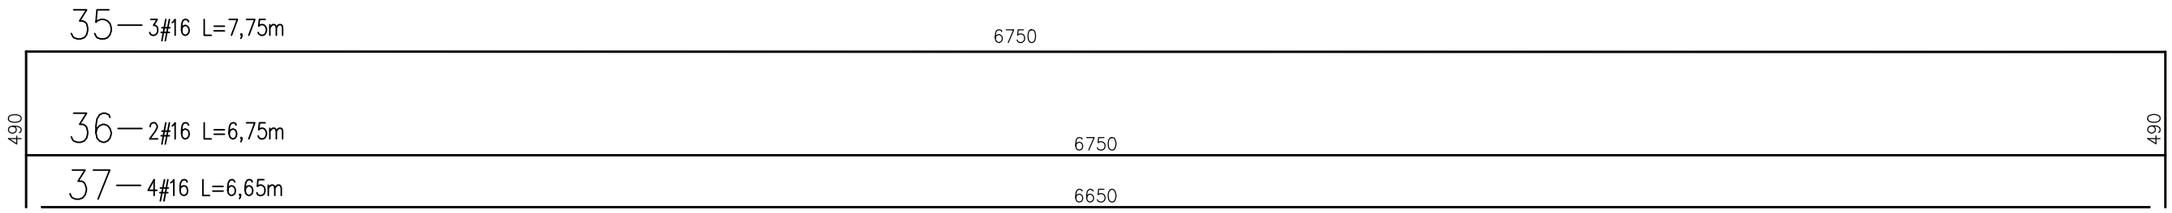
## A-A

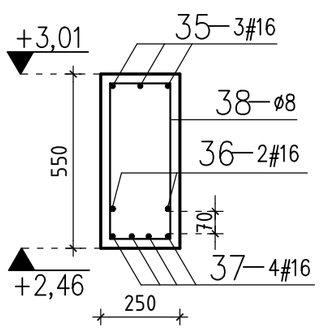


| | |
|---|---|
| Beton | C20/25 (B25) |
| Stal zbrojeniowa | A-IIIN (RB500W) |
| Stal strzemion | A-I |
| Otulina | 2.5cm |

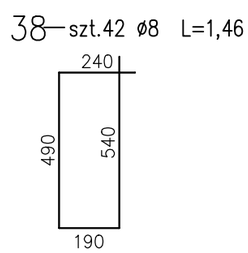
JEDNOSTKA OPRACOWUJĄCA:
TE-DE SP.Z O.O.
ul. Nowy Świat 33/13; 00-029 Warszawa; tel. 605 255 383;
NIP 5252891372; mail: drozdzielpiotr@gmail.com


PT

INWESTOR:
DOMINIK I MARTA GRELA
UL. PIŁSUDSKIEGO 15A
23-400 BIŁGORAJ


NAZWA I ADRES OBIEKTU:
BUDOWA BUDYNKU MIESZKALNEGO JEDNORODZINNEGO WRAZ Z WEWNĘTRZNĄ INSTALACJĄ ELEKTRYCZNĄ, WODNĄ, KANALIZACJI SANITARNEJ, WENTYLACJI MECHANICZNEJ ORAZ ZEWNĘTRZNĄ INSTALACJĄ KABLOWĄ ELEKTROENERGETYCZNĄ NN ZALICZNIKOWĄ, INSTALACJĄ WODOCIĄGOWĄ I KANALIZACYJNĄ
dz. nr 95/9, AR_12; obręb ewidencyjny: 0001 BIŁGORAJ
jednostka ewidencyjna: 060201_1 BIŁGORAJ miasto


| TYTUŁ RYSUNKU | PODCIĄG P-5 | SKALA 1:20 |
|---|---|---|
| FUNKCJA | IMIĘ I NAZWISKO ORAZ ZAKRES I SPECJALNOŚĆ UPRAWNIEŃ | PODPIS |
| PROJEKTANT KONSTRUKCJA | mgr inż. Piotr Droździel<br>*upr. bud. do projektowania i kierowania robotami bez ograniczeń w specj. konstrukcyjno – budowlanej LUB/0364/PWBKb/15* | DATA 12.2025 |
| | | NR RYS. 17 |

# PODCIĄG P-6


SKALA 1:20


SZT. 1

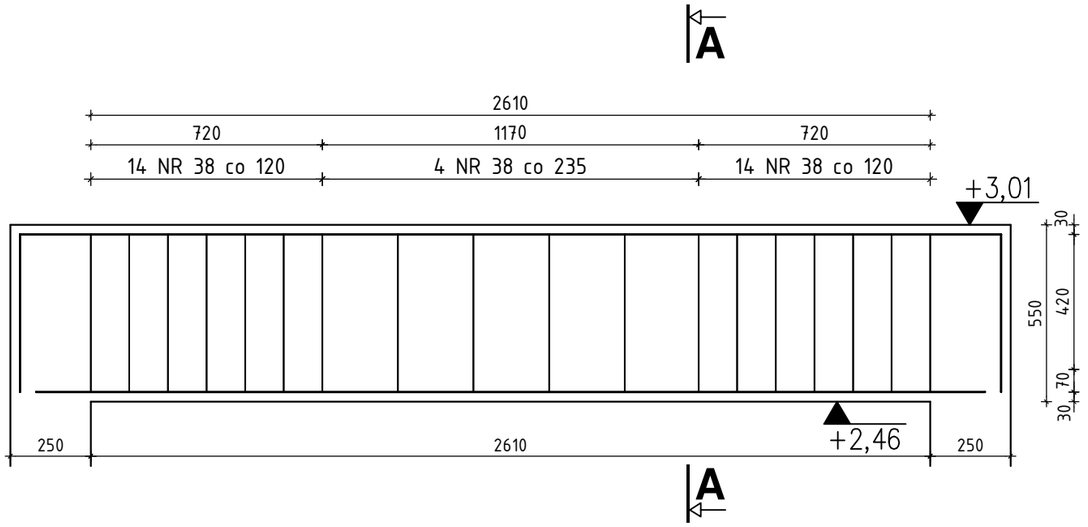

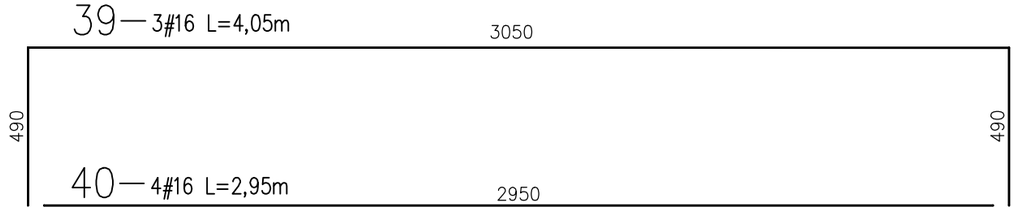
## A-A

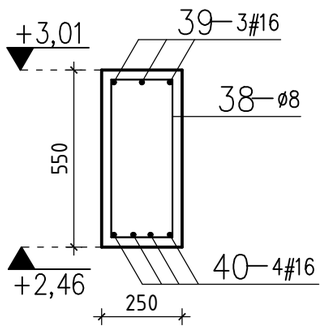


| | |
|---|---|
| Beton | C20/25 (B25) |
| Stal zbrojeniowa | A-IIIN (RB500W) |
| Stal strzemion | A-I |
| Otulina | 2.5cm |

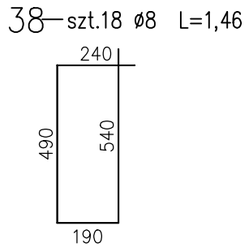
JEDNOSTKA OPRACOWUJĄCA:
TE-DE SP.ZO.O.
ul. Nowy Świat 33/13; 00-029 Warszawa; tel. 605 255 383;
NIP 5252891372; mail: drozdzielpiotr@gmail.com



PT

INWESTOR:
DOMINIK I MARTA GRELA
UL. PIŁSUDSKIEGO 15A
23-400 BIŁGORAJ

NAZWA I ADRES OBIEKTU:
BUDOWA BUDYNKU MIESZKALNEGO JEDNORODZINNEGO WRAZ Z WEWNĘTRZNĄ INSTALACJĄ ELEKTRYCZNĄ, WODNĄ, KANALIZACJI SANITARNEJ, WENTYLACJI MECHANICZNEJ ORAZ ZEWNĘTRZNĄ INSTALACJĄ KABLOWĄ ELEKTROENERGETYCZNĄ NN ZALICZNIKOWĄ, INSTALACJĄ WODOCIĄGOWĄ I KANALIZACYJNĄ
dz. nr 95/9, AR_12; obręb ewidencyjny: 0001 BIŁGORAJ
jednostka ewidencyjna: 060201_1 BIŁGORAJ miasto

| TYTUŁ RYSUNKU | PODCIĄG P-6 | SKALA 1: 20 |
|---|---|---|

| FUNKCJA | IMIĘ I NAZWISKO ORAZ ZAKRES I SPECJALNOŚĆ UPRAWNIEŃ | PODPIS | |
|---|---|---|---|
| PROJEKTANT KONSTRUKCJA | mgr inż. Piotr Droździel<br>*upr. bud. do projektowania i kierowania robotami bez ograniczeń w specj. konstrukcyjno – budowlanej LUB/0364/PWBKb/15* | | DATA 12.2025 |
| | | | NR RYS. 18 |

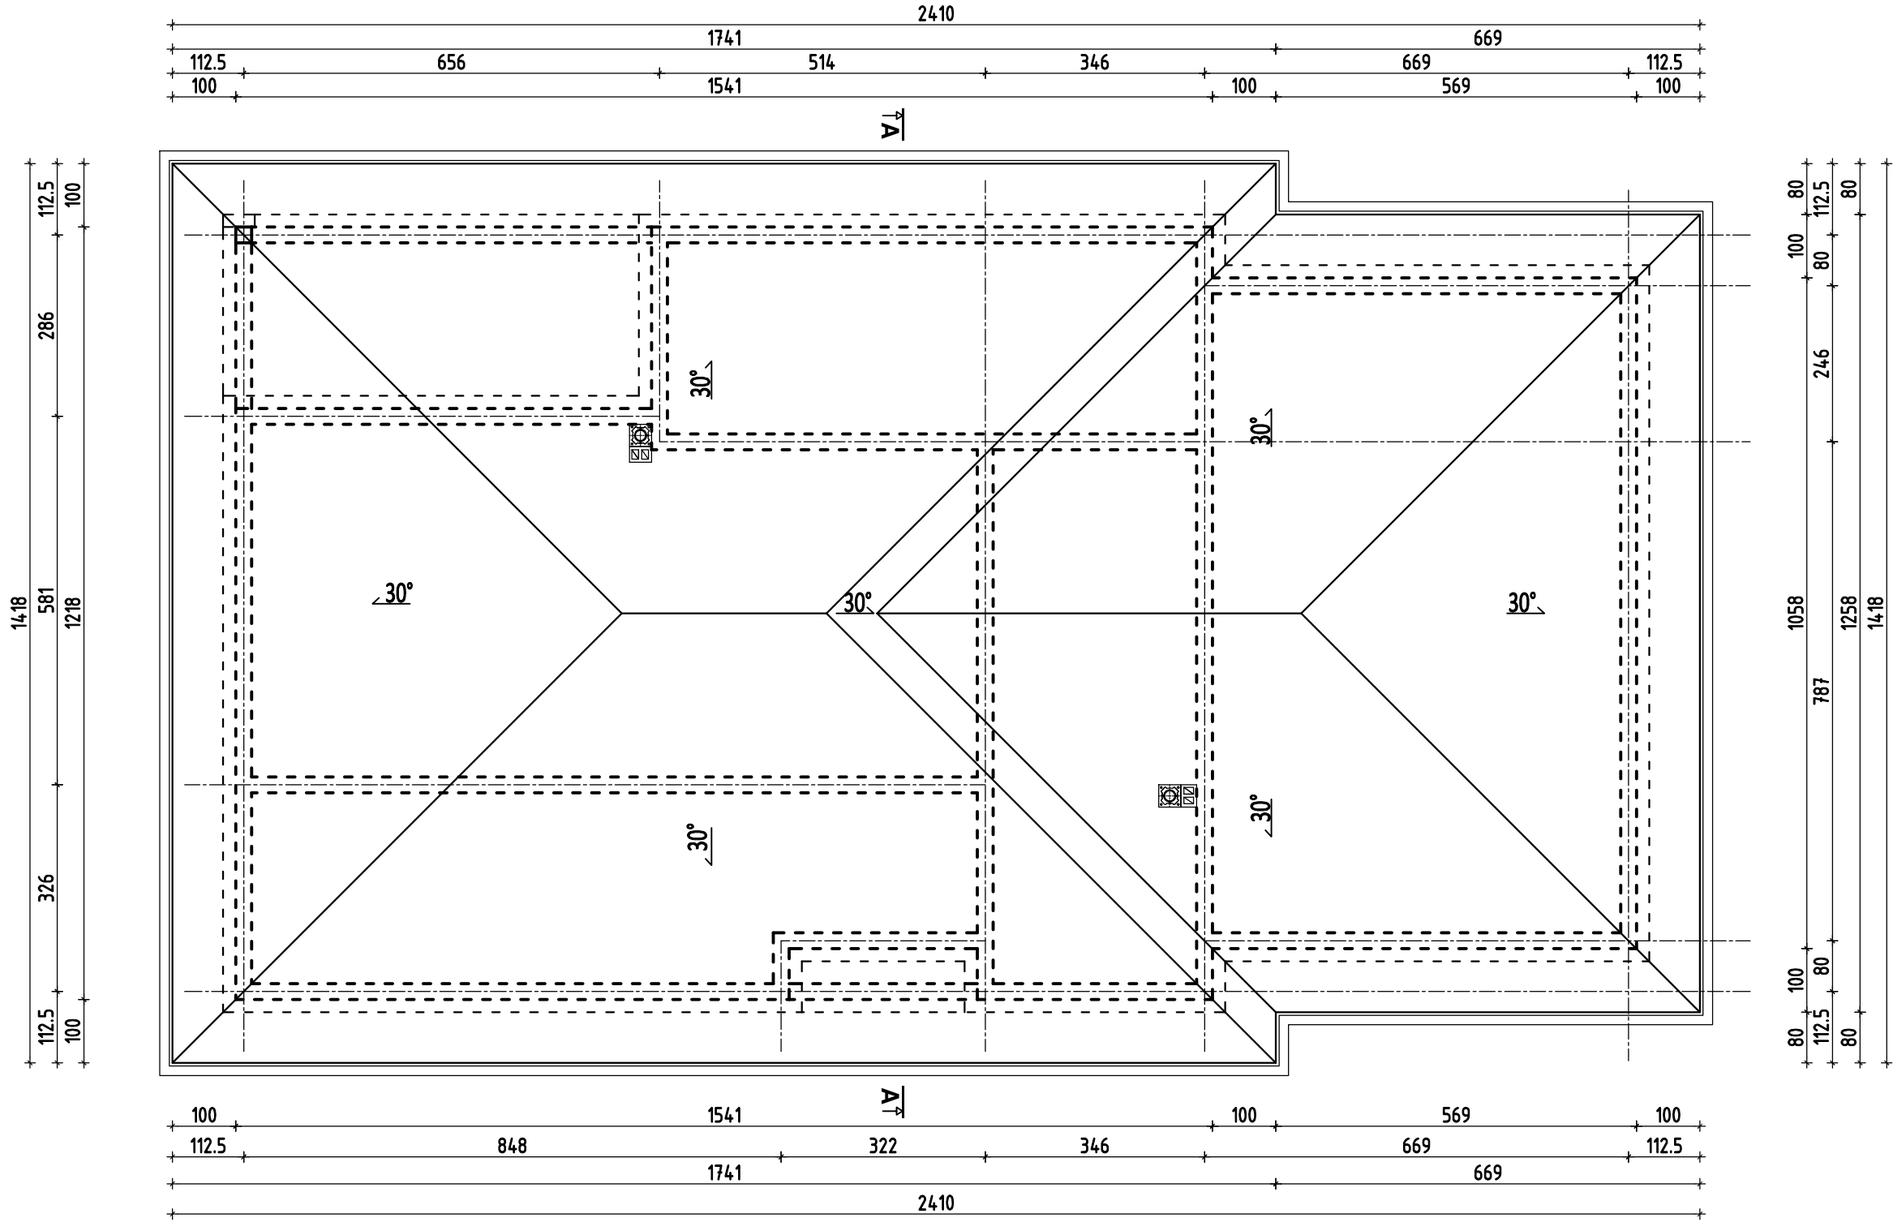




JEDNOSTKA OPRACOWUJĄCA:
TE-DE SP.ZO.O.
ul. Nowy Świat 33/13; 00-029 Warszawa; tel. 605 255 383;
NIP 5252891372; mail: drozdzielpiotr@gmail.com


PT

INWESTOR:
DOMINIK I MARTA GRELA
UL. PIŁSUDSKIEGO 15A
23-400 BIŁGORAJ

NAZWA I ADRES OBIEKTU:
BUDOWA BUDYNKU MIESZKALNEGO JEDNORODZINNEGO WRAZ Z WEWNĘTRZNĄ INSTALACJĄ ELEKTRYCZNĄ, WODNĄ, KANALIZACJI SANITARNEJ, WENTYLACJI MECHANICZNEJ ORAZ ZEWNĘTRZNĄ INSTALACJĄ KABLOWĄ ELEKTROENERGETYCZNĄ NN ZALICZNIKOWĄ, INSTALACJĄ WODOCIĄGOWĄ I KANALIZACYJNĄ
dz. nr 95/9, AR_12; obręb ewidencyjny: 0001 BIŁGORAJ
jednostka ewidencyjna: 060201_1 BIŁGORAJ miasto

| TYTUŁ RYSUNKU | RZUT POŁACI DACHOWEJ | | SKALA 1:100 |
|---|---|---|---|
| FUNKCJA | IMIĘ I NAZWISKO ORAZ ZAKRES I SPECJALNOŚĆ UPRAWNIEŃ | PODPIS | |
| PROJEKTANT KONSTRUKCJA | mgr inż. Piotr Droździel<br>*upr. bud. do projektowania i kierowania robotami bez ograniczeń w specj. konstrukcyjno – budowlanej LUB/0364/PWBKb/15* | | DATA 12.2025 |
| | | | NR RYS. 19 |

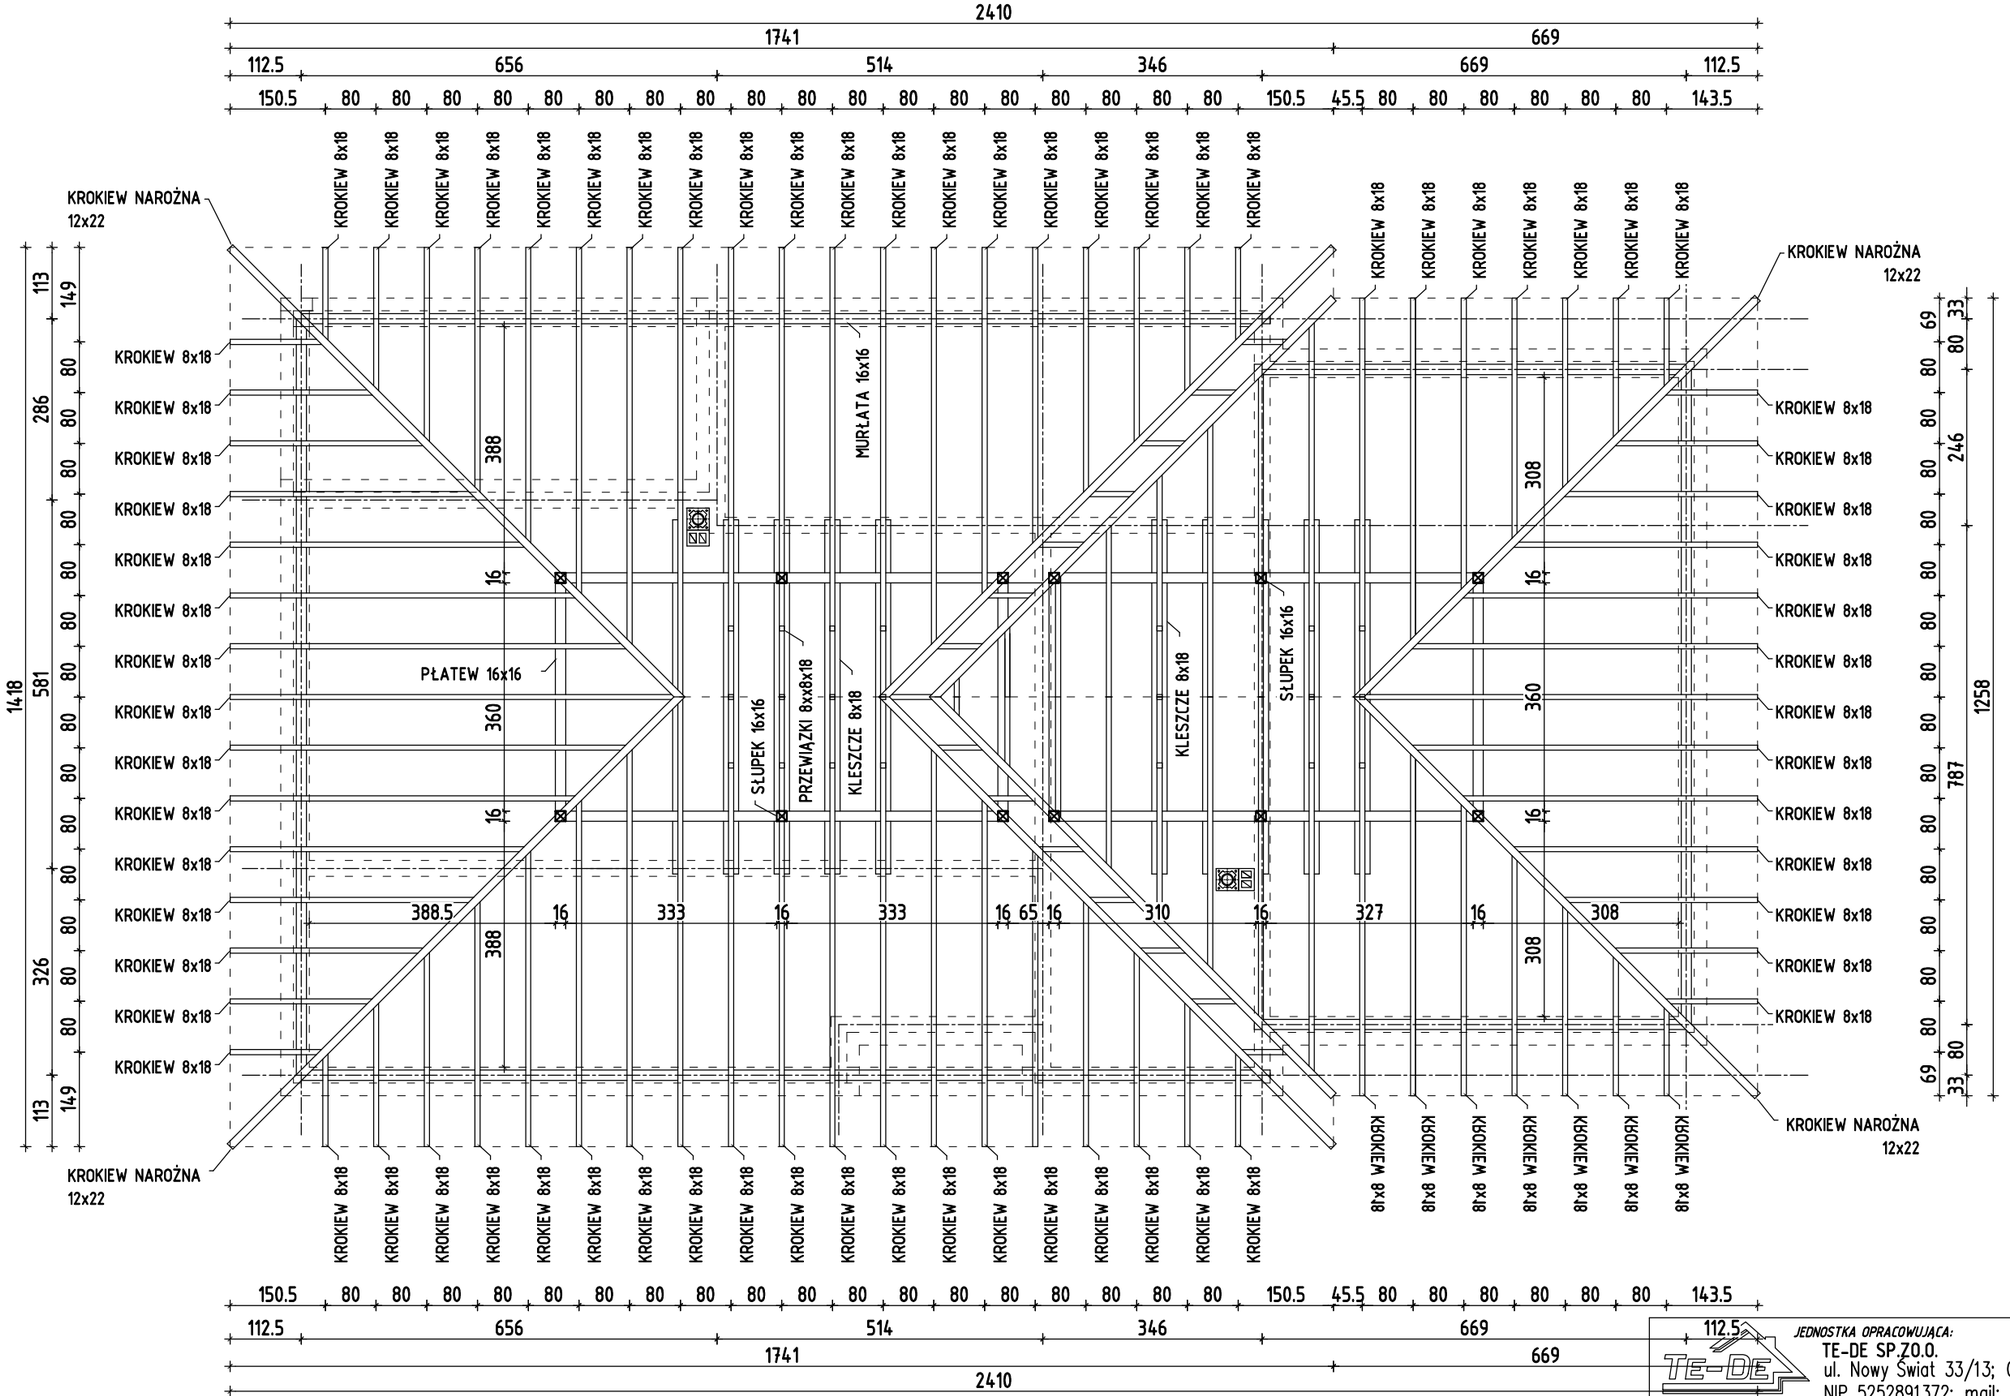


UWAGI:
1. DREWNO C24.
2. MURŁATĘ KOTWIĆ CO 1,0-1,2 m W WIENIEC.
3. KĄT DACHU 30°.
4. WSZYSTKIE ELEMENTY DREWNIANE NA STYKU ZE ŚCIANĄ MUROWANĄ IZOLOWAĆ WARSTWĄ PAPY.
5. ELEMENTY DREWNIANE ZNAJDUJĄCE SIĘ DO 30 CM OD PRZEWODÓW SPALINOWYCH I DYMOWYCH NALEŻY OBŁOŻYĆ OKŁADZINĄ 25 MM TYNKU NA SIATCE.


JEDNOSTKA OPRACOWUJĄCA:
TE-DE SP.ZO.O.
ul. Nowy Świat 33/13; 00-029 Warszawa; tel. 605 255 383;
NIP 5252891372; mail: drozdzielpiotr@gmail.com


PT

INWESTOR:
DOMINIK I MARTA GRELA
UL. PIŁSUDSKIEGO 15A
23-400 BIŁGORAJ

NAZWA I ADRES OBIEKTU:
BUDOWA BUDYNKU MIESZKALNEGO JEDNORODZINNEGO WRAZ Z WEWNĘTRZNĄ INSTALACJĄ ELEKTRYCZNĄ, WODNĄ, KANALIZACJI SANITARNEJ, WENTYLACJI MECHANICZNEJ ORAZ ZEWNĘTRZNĄ INSTALACJĄ KABLOWĄ ELEKTROENERGETYCZNĄ NN ZALICZNIKOWĄ, INSTALACJĄ WODOCIĄGOWĄ I KANALIZACYJNĄ
dz. nr 95/9, AR_12; obręb ewidencyjny: 0001 BIŁGORAJ
jednostka ewidencyjna: 060201_1 BIŁGORAJ miasto

| TYTUŁ RYSUNKU | RZUT WIĘŹBY DACHOWEJ | SKALA 1:100 |
|---|---|---|
| FUNKCJA | IMIĘ I NAZWISKO ORAZ ZAKRES I SPECJALNOŚĆ UPRAWNIEŃ | PODPIS |
| PROJEKTANT KONSTRUKCJA | mgr inż. Piotr Droździel<br>*upr. bud. do projektowania i kierowania robotami bez ograniczeń w spec. konstrukcyjno – budowlanej LUB/0364/PWBKb/15* | DATA 12.2025 |
| | | NR RYS. 20 |